ALJEEL ARCHITECTURE

Design Supervision Project Management

Client name :سعود محمد سعود المسعود

Project name :فيلا سكنية

Project status :Initial Presentation

Date :27 MAY 2024

Saudi Arabia 6071 King Abdulaziz.rd,Fx.+966-11-269-0811

www.ALJEEL-Arch.com

7/14/2024 10:56:49 AM

SHEET LIST	
SHEET NUMBER	**SHEET NAME**
A100	COVER PAGE
A101	SHEET LIST
A102	LEGEND & SYMBOL
A103	AREA
A104	SITE PLAN
A105	GROUND FLOOR PLAN
A106	FIRST FLOOR PLAN
A107	ROOF FLOOR PLAN
A0107	UPPER ROOF FLOOR PLAN
A108	EAST ELEVATION
A109	NORTH ELEVATION
A110	SOUTH ELEVATION
A111	WEST ELEVATION
A112	SECTION A-A
A113	SECTION B-B
A114	PRESPECTIVE SHOT
A115	PERSPECTIVE RENDER
A116	DOOR SCHEDULE
A117	PERSPECTIVE RENDER-2
A118	WINDOW SCHEDULE PG-2
A120	FINAL PAGE

GENERAL NOTES:

1. ALL DIMENSION SHOWN HEREIN ARE ALL IN METERS, UNLESS OR OTHERWISE IT IS SPECIFIED

2. WINDOWS AND WINDOW SCREEN OPENING ON THE JOBSITE AND SUBMIT THE SHOP DRAWINGS PRIOR TO FABRICATION AND INSTALLTION.

3. ALL SHOP DRAWING, SAMPLES, CATALOG CUTOUTS, ETC. TO BE APPROVED BY THE ARCHITECT BEFORE FINAL EXECUTION.

4. REFER TO MECHANICAL, PLUMBING DRAWING FOR AN EXACT LOCATION AND SIZES OF ALL MECHANICAL ELEMENTS SHOWN ON CEILING AND ROOF PLANS.

5. LIGHTING FIXTURE TO BE COORDINATED WITH AN ARCHITECT.

6.ANY DISCREPANCY ON SITE AND ON SHOP DRAWINGS, REFER TO CONSULTING ARCHITECT.

7. FOR DOORS, WINDOWS AND ROOM FINISHING SCHEDULE REFER TO DRAWING NO.___

8. CONTRACTOR SHALL VERIFY ALL STRUCTURAL CONDITIONS AND DETAILS PRIOR TO FINAL EXECUTION AND TO ANY DEMOLITION.

9. FOR ALL PERMANENT STRUCTURAL ELEMENTS, REFER TO STRUCTURAL DRAWINGS.

10. MINIMUN PARKING SPACE IS 2.50M WIDTH AND 5.50M LENGTH.

11.

12. INSTALLATION OF ALL MECHANICAL, ELECTRICAL AND PLUMBING ELEMENTS SHALL BE REFER TO MANUFACTURER'S MANUAL.

13. OR UNLESS OTHERWISE BE SPECIFIED

THE INTERIOR DESIGN:
FOR THE FOLLOWING ITEMS:
-CEILING
-DOOR & WINDOW
-FINISHING
-TOILET (WALL TILLING)
-SKYLIGHT
-HANDRAILS

KEYPLAN:

OFFICIAL STAMP:

☐ FINAL
☐ FOR CONSTRUCTION
☐ AS-BUILT
☐ APPROVED AS NOTED
☐ FOR MUNICIPALITIES
☐ OTHERS

DISCIPLINE:
A R C H I T E C T U R E

PROJECT:
فيلا سكنية

OWNER:
سعود محمد سعود المسعود

ALJEEL ARCHITECTS
Design - Project Management - Supervision
6071 King Abdulaziz.Rd- Riyadh - Saudi Arabia
Tel:+966-11-269-0811
WWW.ALJEEL-ARCH.COM

DRAWING TITLE:
SHEET LIST

SHEET NO.: A101
SCALE:

DESIGNED BY:	APPROVED BY:	DRAWN BY:	DATE:
Arch. Saleh	Arch. Saleh	Utman	03/03/22
PROJECT NO.:	**STATUS:**	**REVISION**	**CODE:**
Al-Jeel 104	Initial Presentation	---	

7/14/2024 10:56:50 AM

C:\Users\Mohammed\ALJEEL ARCHITECTS Dropbox\design\Aljeel office Dropbox\Running Projects\213-فيلا سعود\Design\Arch\Rvt\VILLA SAUD UPDATE NEW FOR BAADIYA.rvt

ABBREVIATIONS

A	
A/C	AIR CONDITIONING
AD	AREA DRAIN
AFF	ABOVE FINISH FLOOR
AFC	ABOVE FALSE CEILING
AHU	AIR HANDLING UNIT
ALUM	ALUMINUM
ANOD	ANODIZED
APPROX	APPROXIMATELY
AR	ARCHITECTURAL
B	
BD	BIDET
BT	BATH TUB
BLDG	BUILDING
BOT.O.	BOTTOM OF
B.O.S.S.	BOTTOM OF STRUCTURAL SLAB
BSMT	BASEMENT
BV	BLAST VALVE
C	
CLG	CEILING
CH	CEILING HEIGHT
CEM	CEMENT
CL	CENTER LINE
COL	COLUMN
CONC	CONCRETE
CONT	CONTINUOUS
CMU	CONCRETE MASONRY UNIT
COMM	COMMUNICATION
D	
DET	AIR CONDITIONING
DH	AREA DRAIN
DHH	ABOVE FINISH FLOOR
DIA	ABOVE FALSE CEILING
DIM	AIR HANDLING UNIT
DN	ALUMINUM
DR	ANODIZED
DRN	APPROXIMATELY
DW	ARCHITECTURAL
DWG	
E	
E	EAST, EASTING
EL	ELEVATION
ELEC	ELECTRIC
EQ	EQUAL
EQPT	EQUIPMENT
EXP	EXPANSION
EJ	EXPANSION JOINT
EXT	EXTERIOR

F	
F	FIXED
FD	FLOOR DRAIN
FCO	FLOOR CLEAN OUT
FCL	FINISH CEILING LEVEL
FFL	FINISH FLOOR LEVEL
FGL	FINISH GRADE LEVEL
FRL	FINISH ROOF LEVEL
FHC	FIRE HOSE CABINET
FHR	FIRE HOSE REEL
FIN	FINISH
FLR	FLOOR
FP	FIXED PANEL
FR	FIRE RESISTIVE
FH	FIRE HYDRANT
F/A	FROM ABOVE
G	
GALV	GALVANIZED
G.I.	GALVANIZED IRON
GEN	GENERAL
GLS	GLASS
GRC	GLASS FIBER REINFORCED CEMENT
GRD	GROUND
GRG	GLASS FIBER REINFORCED GYPSUM
GYP BD	GYPSUM BOARD
H	
HR	HOUR
HT	HEIGHT
HW	HARDWARE
HWS	HOT WATER SUPPLY
I	
ID	INTERIOR DESIGN
INT	INTERIOR
J	
JAN	JANITOR
JT	JOINT
K	
KS	KITCHEN SINK
L	
L	LENGTH
LAV	LAVATORY
LEV	LEVEL
LS	LANDSCAPE
LTG	LIGHTING

M	
M	METER
MACH	MACHINE
MAX	MAXIMUM
MDF	MEDIUM DENSITY FIBERBOARD
MECH	MECHANICAL
MET	METAL
MEZZ	MEZZANINE
MFTR	MANUFACTURER
MH	MANHOLE
MID	MIDDLE
MIN	MINIMUM
MM	MILLIMETER
MO	MASONRY OPENING
MVP	MAIN VENT PIPE
N	
N	AIR CONDITIONING
NIC	AREA DRAIN
NO	ABOVE FINISH FLOOR
NTS	ABOVE FALSE CEILING
O	
OC	ON CENTER
OP	OVERFLOW
OPNG	OPENING
OH	OVERHEAD
P	
PACU	PACKAGE AIR CONDITIONING UNIT
PART	PARTITION
PC	PRECAST
PLAS	PLASTER
PL	PLATE
PLYBD	PLYBOARD
PLUMB	PLUMBING
PNL	PANEL
PR	PAIR
PTG	PLANTING
R	
R	RADIUS
RAC	ROOM AIR CONDITIONER
RC	REINFORCED CONCRETE
RD	ROOF DRAIN
RE	REFER
REQ	REQUIRED
RF	RESILIANT FLOORING
REV	REVISION
RM	ROOM
RP	ROOF PENETRATION
RWO	RAIN WATER OUTLET
RWP	RAIN WATER PIPE

HATCH / MATERIAL

- SAND, SCREED
- PLASTER OR RENDER PAINTED
- METAL (SECTION)
- ROUGH TIMBER
- FINISHED TIMBER
- PLYWOOD
- SYPOREX PRE-CAST WALL
- SEALANT, RUBBER AND PLASTIC
- GYPSUM PLASTERBOARD, MINERAL FIBRE
- CARPET
- CONCRETE BLOCK WALL
- LOW HEIGHT PARTITION WALL
- REINFORCED CONCRETE
- REINFORCED CONCRETE (SMALL SCALE)
- PRE CAST CONCRETE
- STEEL AND IRON (LARGE SCALE)
- EARTH
- INSULATION (LOOSE)

GENERAL NOTES

1. ALL DIMENSIONS ARE IN MILLIMETERS AND LEVELS IN METERS UNLESS OTHERWISE NOTED.
2. TYPICAL DETAILS SHALL BE READ IN CONJUNCTION WITH THE APPROPRIATE ARCHITECTURAL/CIVIL AND SERVICES DRAWINGS.
3. THE DRAWINGS SHALL NOT BE SCALED. ONLY WRITTEN DIMENSIONS SHALL BE USED.
4. THE CONTRACTOR SHALL VERIFY ALL EXISTING CONDITIONS ON SITE AND SECURE NECESSARY PERMITS FOR CONSTRUCTION.
5. THE CONTRACTOR WILL BE RESPONSIBLE FOR ALL SETTING OUT AND IS DEEMED TO HAVE CHECKED THE DESIGN.
6. THE CONTRACTOR IS DEEMED TO HAVE ALLOWED RATES FOR ANY ERRORS IN THIS DRAWINGS.
7. THE CONTRACTOR SHALL SUBMIT SHOP DRAWINGS AND SAMPLES OF ALL MATERIALS AND COLORS TO BE APPROVED BY THE CONSULTANT BEFORE COMMENCING ANY WORK.
8. COORDINATION BETWEEN ARCHITECTURAL DRAWINGS AND ALL OTHER ENGINEERING DRAWINGS WILL BE THE MAIN CONTRACTOR RESPONSIBILITY PRIOR TO WORK COMMENCEMENT.
9. A RAISED MARBLE THRESHOLD SHALL BE USED BETWEEN WET AREAS AND ADJACENT FINISHED AREAS.
10. ALL CHANGES IN DIRECTION OF PLASTER AND RENDER SHALL BE FORMED BY THE APPROPRIATE GALVANIZED METAL BEAD.
11. ALL CEILING LEVELS SHOW THE ACTUAL CEILING HEIGHT.
12. ALL MATERIALS AND FINISHES SHALL BE SUBMITTED TO THE SUPERVISING OFFICE FOR APPROVAL BEFORE INSTALLATION.
13. LEVELS OF EXTERNAL FLOORS FINISHES ARE SHOWN AS NOMINAL. FINISHES LAID TO FALL AWAY FROM THE BUILDING.
14. ALL BUILDING LEVELS ARE BASED ON ±0.00 LEVEL.

SYMBOLS & INDICATORS

SECTION

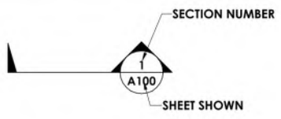

ELEVATIONS

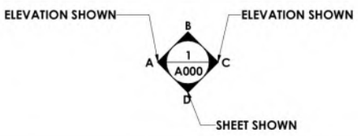

LEVELS

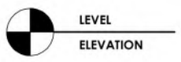

TAGS

SHEET CODE

SHEET/SERIES NUMBER

ENGINEERING DISCIPLINE

A-101

GP	GENERAL LAYOUT
PS	PRIMARY SCHOOL BUILDING
PA	PRIMARY AUXILIARY BUILDING
IS	INTERMEDIATE SCHOOL BUILDING
IA	INTERMEDIATE AUXILIARY BUILDING
SS	SECONDARY SCHOOL BUILDING
SA	SECONDARY AUXILIARY BUILDING

&	AND	**@**	AT
%	PERCENT	**□**	CENTER LINE
□	DIAMETER	**#**	NUMBER APPROXIMATE

DRAWING SERIES KEY

SERIES	ARCHITECTURAL A	STRUCTURAL S	ELECTRICAL E	MECHANICAL M	PLUMBING P
000	GENERAL DWGS				
100	FLOOR PLANS				
200	ELEVATIONS & SECTIONS				
300	FLOOR PATTERN				
400	REFLECTED CEILING PLANS				
500	STAIR DETAILS				
600	WET AREA DETAILS				
700	DOORS, WINDOWS & OPENINGS SCHEDULES				
800	FURNITURE LAYOUT				
900	FINISHES SCHEDULES				
950	MISCELLANEOUS DETAILS				

GENERAL NOTES:

1. ALL DIMENSION SHOWN HEREIN ARE ALL IN METERS, UNLESS OR OTHERWISE IT IS SPECIFIED

2. WINDOWS AND WINDOW SCREEN OPENING ON THE JOBSITE AND SUBMIT THE SHOP DRAWINGS PRIOR TO FABRICATION AND INSTALLTION.

3. ALL SHOP DRAWING, SAMPLES, CATALOG CUTOUTS, ETC. TO BE APPROVED BY THE ARCHITECT BEFORE FINAL EXECUTION.

4. REFER TO MECHANICAL, PLUMBING DRAWING FOR AN EXACT LOCATION AND SIZES OF ALL MECHANICAL ELEMENTS SHOWN ON CEILING AND ROOF PLANS.

5. LIGHTING FIXTURE TO BE COORDINATED WITH AN ARCHITECT.

6.ANY DISCREPANCY ON SITE AND ON SHOP DRAWINGS, REFER TO CONSULTING ARCHITECT.

7. FOR DOORS, WINDOWS AND ROOM FINISHING SCHEDULE REFER TO DRAWING NO.___

8. CONTRACTOR SHALL VERIFY ALL STRUCTURAL CONDITIONS AND DETAILS PRIOR TO FINAL EXECUTION AND TO ANY DEMOLITION.

9. FOR ALL PERMANENT STRUCTURAL ELEMENTS, REFER TO STRUCTURAL DRAWINGS.

10. MINIMUN PARKING SPACE IS 2.50M WIDTH AND 5.50M LENGTH.

11.

12. INSTALLATION OF ALL MECHANICAL, ELECTRICAL AND PLUMBING ELEMENTS SHALL BE REFER TO MANUFACTURER'S MANUAL.

13. OR UNLESS OTHERWISE BE SPECIFIED

THE INTERIOR DESIGN:
FOR THE FOLLOWING ITEMS:
-CEILING
-DOOR & WINDOW
-FINISHING
-TOILET (WALL TILLING)
-SKYLIGHT
-HANDRAILS

KEYPLAN:

OFFICIAL STAMP:

- ☐ FINAL
- ☐ FOR CONSTRUCTION
- ☐ AS-BUILT
- ☐ APPROVED AS NOTED
- ☐ FOR MUNICIPALITIES
- ☐ OTHERS

DISCIPLINE: ARCHITECTURE

PROJECT: فيلا سكنية

OWNER: سعود محمد سعود المسعود

ALJEEL ARCHITECTS
Design - Project Management - Supervision
6071 King Abdulaziz.Rd- Riyadh - Saudi Arabia
Tel:+966-11-269-0811
WWW.ALJEEL-ARCH.COM

DRAWING TITLE: **LEGEND & SYMBOL**

SHEET NO.: A102

SCALE:

DESIGNED BY:	APPROVED BY:	DRAWN BY:	DATE:
Arch. Saleh	Arch. Saleh	Utman	08/02/22
PROJECT NO.:	**STATUS:**	**REVISION**	**CODE:**
Al-Jeel 104	Initial Presentation	---	

7/14/2024 10:56:50 AM

C:\Users\Mohammed\ALJEEL ARCHITECTS Dropbox\design\Aljeel office Dropbox\Running Projects\213-فيلا سعود\Design\Arch\Rvt\VILLA SAUD UPDATE NEW FOR BAADIYA.rvt

جدول المساحات				
مساحة الارض 750.00				
الدور	المساحة	النسبة	الوحدات	الغرض
مساحة الدور الارضي	445.90	% 59.45	1	سكني
مساحة الدور الاول	245.60	% 32.74	0	سكني
مساحة الدور الثاني	122.85	% 50.00 من الدور الاول	0	سكني
اسوار	110.00 م ط			

ارتدادت المشروع			
الجهة	الحدود	الابعاد	الارتداد
الشمال	جار	25.00	2.00
الشرق	شارع عرض 15 م	30.00	12.40
الجنوب	شارع عرض 20 م	25.00	2.00
الغرب	جار	30.00	1.20

المالك	سعود محمد سعود المسعود		
مشروع	فيلا سكنية		
الحي	العاصمة		
رقم الصك	460001203533		
رقم القطعة	80	رقم المخطط	2899

GENERAL NOTES:

1. ALL DIMENSION SHOWN HEREIN ARE ALL IN METERS, UNLESS OR OTHERWISE IT IS SPECIFIED

2. WINDOWS AND WINDOW SCREEN OPENING ON THE JOBSITE AND SUBMIT THE SHOP DRAWINGS PRIOR TO FABRICATION AND INSTALLTION.

3. ALL SHOP DRAWING, SAMPLES, CATALOG CUTOUTS, ETC. TO BE APPROVED BY THE ARCHITECT BEFORE FINAL EXECUTION.

4. REFER TO MECHANICAL, PLUMBING DRAWING FOR AN EXACT LOCATION AND SIZES OF ALL MECHANICAL ELEMENTS SHOWN ON CEILING AND ROOF PLANS.

5. LIGHTING FIXTURE TO BE COORDINATED WITH AN ARCHITECT.

6.ANY DISCREPANCY ON SITE AND ON SHOP DRAWINGS, REFER TO CONSULTING ARCHITECT.

7. FOR DOORS, WINDOWS AND ROOM FINISHING SCHEDULE REFER TO DRAWING NO.___

8. CONTRACTOR SHALL VERIFY ALL STRUCTURAL CONDITIONS AND DETAILS PRIOR TO FINAL EXECUTION AND TO ANY DEMOLITION.

9. FOR ALL PERMANENT STRUCTURAL ELEMENTS, REFER TO STRUCTURAL DRAWINGS.

10. MINIMUN PARKING SPACE IS 2.50M WIDTH AND 5.50M LENGTH.

11.

12. INSTALLATION OF ALL MECHANICAL, ELECTRICAL AND PLUMBING ELEMENTS SHALL BE REFER TO MANUFACTURER'S MANUAL.

13. OR UNLESS OTHERWISE BE SPECIFIED

THE INTERIOR DESIGN:
FOR THE FOLLOWING ITEMS:
-CEILING
-DOOR & WINDOW
-FINISHING
-TOILET (WALL TILLING)
-SKYLIGHT
-HANDRAILS

KEYPLAN:

OFFICIAL STAMP:

- [ ] FINAL
- [ ] FOR CONSTRUCTION
- [ ] AS-BUILT
- [ ] APPROVED AS NOTED
- [ ] FOR MUNICIPALITIES
- [ ] OTHERS

DISCIPLINE:
ARCHITECTURE

PROJECT:
فيلا سكنية

OWNER:
سعود محمد سعود المسعود

ALJEEL ARCHITECTS
Design - Project Management - Supervision
6071 King Abdulaziz.Rd- Riyadh - Saudi Arabia
Tel:+966-11-269-0811
WWW.ALJEEL-ARCH.COM

DRAWING TITLE:
AREA

SHEET NO.: A103
SCALE: 1 : 90

DESIGNED BY:	APPROVED BY:	DRAWN BY:	DATE:
Arch. Saleh	Arch. Saleh	Utman	10/09/23
PROJECT NO.:	STATUS:	REVISION	CODE:
Al-Jeel 104	Initial Presentation	---	

7/14/2024 10:56:52 AM

C:\Users\Mohammed\ALJEEL ARCHITECTS Dropbox\design\Aljeel office Dropbox\Running Projects\213-فيلا سعود\Design\Arch\Rvt\VILLA SAUD UPDATE NEW FOR BAADIYA.rvt

GENERAL NOTES:

1. ALL DIMENSION SHOWN HEREIN ARE ALL IN METERS, UNLESS OR OTHERWISE IT IS SPECIFIED

2. WINDOWS AND WINDOW SCREEN OPENING ON THE JOBSITE AND SUBMIT THE SHOP DRAWINGS PRIOR TO FABRICATION AND INSTALLTION.

3. ALL SHOP DRAWING, SAMPLES, CATALOG CUTOUTS, ETC. TO BE APPROVED BY THE ARCHITECT BEFORE FINAL EXECUTION.

4. REFER TO MECHANICAL, PLUMBING DRAWING FOR AN EXACT LOCATION AND SIZES OF ALL MECHANICAL ELEMENTS SHOWN ON CEILING AND ROOF PLANS.

5. LIGHTING FIXTURE TO BE COORDINATED WITH AN ARCHITECT.

6.ANY DISCREPANCY ON SITE AND ON SHOP DRAWINGS, REFER TO CONSULTING ARCHITECT.

7. FOR DOORS, WINDOWS AND ROOM FINISHING SCHEDULE REFER TO DRAWING NO.___

8. CONTRACTOR SHALL VERIFY ALL STRUCTURAL CONDITIONS AND DETAILS PRIOR TO FINAL EXECUTION AND TO ANY DEMOLITION.

9. FOR ALL PERMANENT STRUCTURAL ELEMENTS, REFER TO STRUCTURAL DRAWINGS.

10. MINIMUN PARKING SPACE IS 2.50M WIDTH AND 5.50M LENGTH.

11.

12. INSTALLATION OF ALL MECHANICAL, ELECTRICAL AND PLUMBING ELEMENTS SHALL BE REFER TO MANUFACTURER'S MANUAL.

13. OR UNLESS OTHERWISE BE SPECIFIED

THE INTERIOR DESIGN:

FOR THE FOLLOWING ITEMS:
-CEILING
-DOOR & WINDOW
-FINISHING
-TOILET (WALL TILLING)
-SKYLIGHT
-HANDRAILS

KEYPLAN:

OFFICIAL STAMP:

- [ ] FINAL
- [ ] FOR CONSTRUCTION
- [ ] AS-BUILT
- [ ] APPROVED AS NOTED
- [ ] FOR MUNICIPALITIES
- [ ] OTHERS

DISCIPLINE:
A R C H I T E C T U R E

PROJECT:
فيلا سكنية

OWNER:
سعود محمد سعود المسعود

ALJEEL ARCHITECTS
Design - Project Management - Supervision
6071 King Abdulaziz.Rd- Riyadh - Saudi Arabia
Tel:+966-11-269-0811
WWW.ALJEEL-ARCH.COM

DRAWING TITLE:
PERSPECTIVE RENDER

SHEET NO.: A115

SCALE:

DESIGNED BY:	APPROVED BY:	DRAWN BY:	DATE:
Arch. Saleh	Arch. Saleh	Utman	01/04/24
PROJECT NO.:	**STATUS:**	**REVISION**	**CODE:**
Al-Jeel 104	Initial Presentation	---	

7/14/2024 10:57:02 AM

C:\Users\Mohammed\ALJEEL ARCHITECTS Dropbox\design\Aljeel office Dropbox\Running Projects\213-فيلا سعود\Design\Arch\Rvt\VILLA SAUD UPDATE NEW FOR BAADIYA.rvt

GENERAL NOTES:

1. ALL DIMENSION SHOWN HEREIN ARE ALL IN METERS, UNLESS OR OTHERWISE IT IS SPECIFIED

2. WINDOWS AND WINDOW SCREEN OPENING ON THE JOBSITE AND SUBMIT THE SHOP DRAWINGS PRIOR TO FABRICATION AND INSTALLTION.

3. ALL SHOP DRAWING, SAMPLES, CATALOG CUTOUTS, ETC. TO BE APPROVED BY THE ARCHITECT BEFORE FINAL EXECUTION.

4. REFER TO MECHANICAL, PLUMBING DRAWING FOR AN EXACT LOCATION AND SIZES OF ALL MECHANICAL ELEMENTS SHOWN ON CEILING AND ROOF PLANS.

5. LIGHTING FIXTURE TO BE COORDINATED WITH AN ARCHITECT.

6.ANY DISCREPANCY ON SITE AND ON SHOP DRAWINGS, REFER TO CONSULTING ARCHITECT.

7. FOR DOORS, WINDOWS AND ROOM FINISHING SCHEDULE REFER TO DRAWING NO.___

8. CONTRACTOR SHALL VERIFY ALL STRUCTURAL CONDITIONS AND DETAILS PRIOR TO FINAL EXECUTION AND TO ANY DEMOLITION.

9. FOR ALL PERMANENT STRUCTURAL ELEMENTS, REFER TO STRUCTURAL DRAWINGS.

10. MINIMUN PARKING SPACE IS 2.50M WIDTH AND 5.50M LENGTH.

11.

12. INSTALLATION OF ALL MECHANICAL, ELECTRICAL AND PLUMBING ELEMENTS SHALL BE REFER TO MANUFACTURER'S MANUAL.

13. OR UNLESS OTHERWISE BE SPECIFIED

THE INTERIOR DESIGN:

FOR THE FOLLOWING ITEMS:
-CEILING
-DOOR & WINDOW
-FINISHING
-TOILET (WALL TILLING)
-SKYLIGHT
-HANDRAILS

KEYPLAN:

OFFICIAL STAMP:

- ☐ FINAL
- ☐ FOR CONSTRUCTION
- ☐ AS-BUILT
- ☐ APPROVED AS NOTED
- ☐ FOR MUNICIPALITIES
- ☐ OTHERS

DISCIPLINE:
A R C H I T E C T U R E

PROJECT:
فيلا سكنية

OWNER:
سعود محمد سعود المسعود

ALJEEL ARCHITECTS
Design - Project Management - Supervision
6071 King Abdulaziz.Rd- Riyadh - Saudi Arabia
Tel:+966-11-269-0811
WWW.ALJEEL-ARCH.COM

DRAWING TITLE:
PERSPECTIVE RENDER-2

SHEET NO.: A117
SCALE:

DESIGNED BY:	APPROVED BY:	DRAWN BY:	DATE:
Arch. Saleh	Arch. Saleh	Utman	01/04/24
PROJECT NO.:	STATUS:	REVISION	CODE:
Al-Jeel 104	Initial Presentation	---	

7/14/2024 10:57:04 AM

C:\Users\Mohammed\ALJEEL ARCHITECTS Dropbox\design\Aljeel office Dropbox\Running Projects\213-فيلا سعود\Design\Arch\Rvt\VILLA SAUD UPDATE NEW FOR BAADIYA.rvt

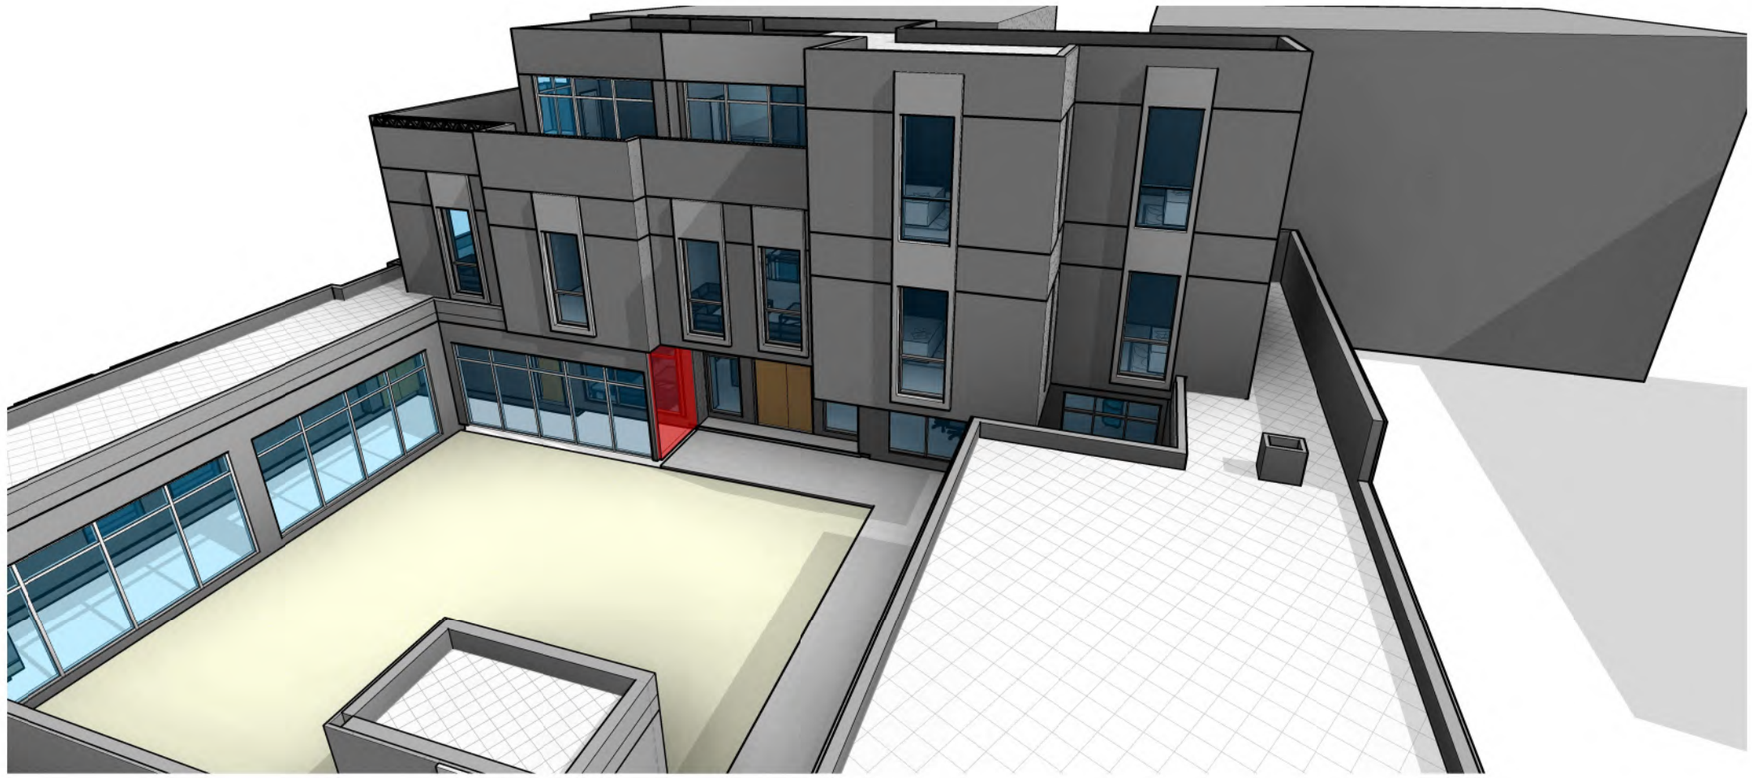

GENERAL NOTES:

1. ALL DIMENSION SHOWN HEREIN ARE ALL IN METERS, UNLESS OR OTHERWISE IT IS SPECIFIED

2. WINDOWS AND WINDOW SCREEN OPENING ON THE JOBSITE AND SUBMIT THE SHOP DRAWINGS PRIOR TO FABRICATION AND INSTALLTION.

3. ALL SHOP DRAWING, SAMPLES, CATALOG CUTOUTS, ETC. TO BE APPROVED BY THE ARCHITECT BEFORE FINAL EXECUTION.

4. REFER TO MECHANICAL, PLUMBING DRAWING FOR AN EXACT LOCATION AND SIZES OF ALL MECHANICAL ELEMENTS SHOWN ON CEILING AND ROOF PLANS.

5. LIGHTING FIXTURE TO BE COORDINATED WITH AN ARCHITECT.

6.ANY DISCREPANCY ON SITE AND ON SHOP DRAWINGS, REFER TO CONSULTING ARCHITECT.

7. FOR DOORS, WINDOWS AND ROOM FINISHING SCHEDULE REFER TO DRAWING NO.___

8. CONTRACTOR SHALL VERIFY ALL STRUCTURAL CONDITIONS AND DETAILS PRIOR TO FINAL EXECUTION AND TO ANY DEMOLITION.

9. FOR ALL PERMANENT STRUCTURAL ELEMENTS, REFER TO STRUCTURAL DRAWINGS.

10. MINIMUN PARKING SPACE IS 2.50M WIDTH AND 5.50M LENGTH.

11.

12. INSTALLATION OF ALL MECHANICAL, ELECTRICAL AND PLUMBING ELEMENTS SHALL BE REFER TO MANUFACTURER'S MANUAL.

13. OR UNLESS OTHERWISE BE SPECIFIED

THE INTERIOR DESIGN:
FOR THE FOLLOWING ITEMS:
-CEILING
-DOOR & WINDOW
-FINISHING
-TOILET (WALL TILLING)
-SKYLIGHT
-HANDRAILS

KEYPLAN:

OFFICIAL STAMP:

- [ ] FINAL
- [ ] FOR CONSTRUCTION
- [ ] AS-BUILT
- [ ] APPROVED AS NOTED
- [ ] FOR MUNICIPALITIES
- [ ] OTHERS

DISCIPLINE:
A R C H I T E C T U R E

PROJECT:
فيلا سكنية

OWNER:
سعود محمد سعود المسعود

ALJEEL ARCHITECTS
Design - Project Management - Supervision
6071 King Abdulaziz.Rd- Riyadh - Saudi Arabia
Tel:+966-11-269-0811
WWW.ALJEEL-ARCH.COM

DRAWING TITLE:
PRESPECTIVE SHOT

SHEET NO.: A114

SCALE:

DESIGNED BY:	APPROVED BY:	DRAWN BY:	DATE:
Arch. Saleh	Arch. Saleh	Utman	12/14/23
PROJECT NO.:	STATUS:	REVISION	CODE:
Al-Jeel 104	Initial Presentation	---	

7/14/2024 10:57:00 AM

C:\Users\Mohammed\ALJEEL ARCHITECTS Dropbox\design\Aljeel office Dropbox\Running Projects\213-فيلا سعود\Design\Arch\Rvt\VILLA SAUD UPDATE NEW FOR BAADIYA.rvt

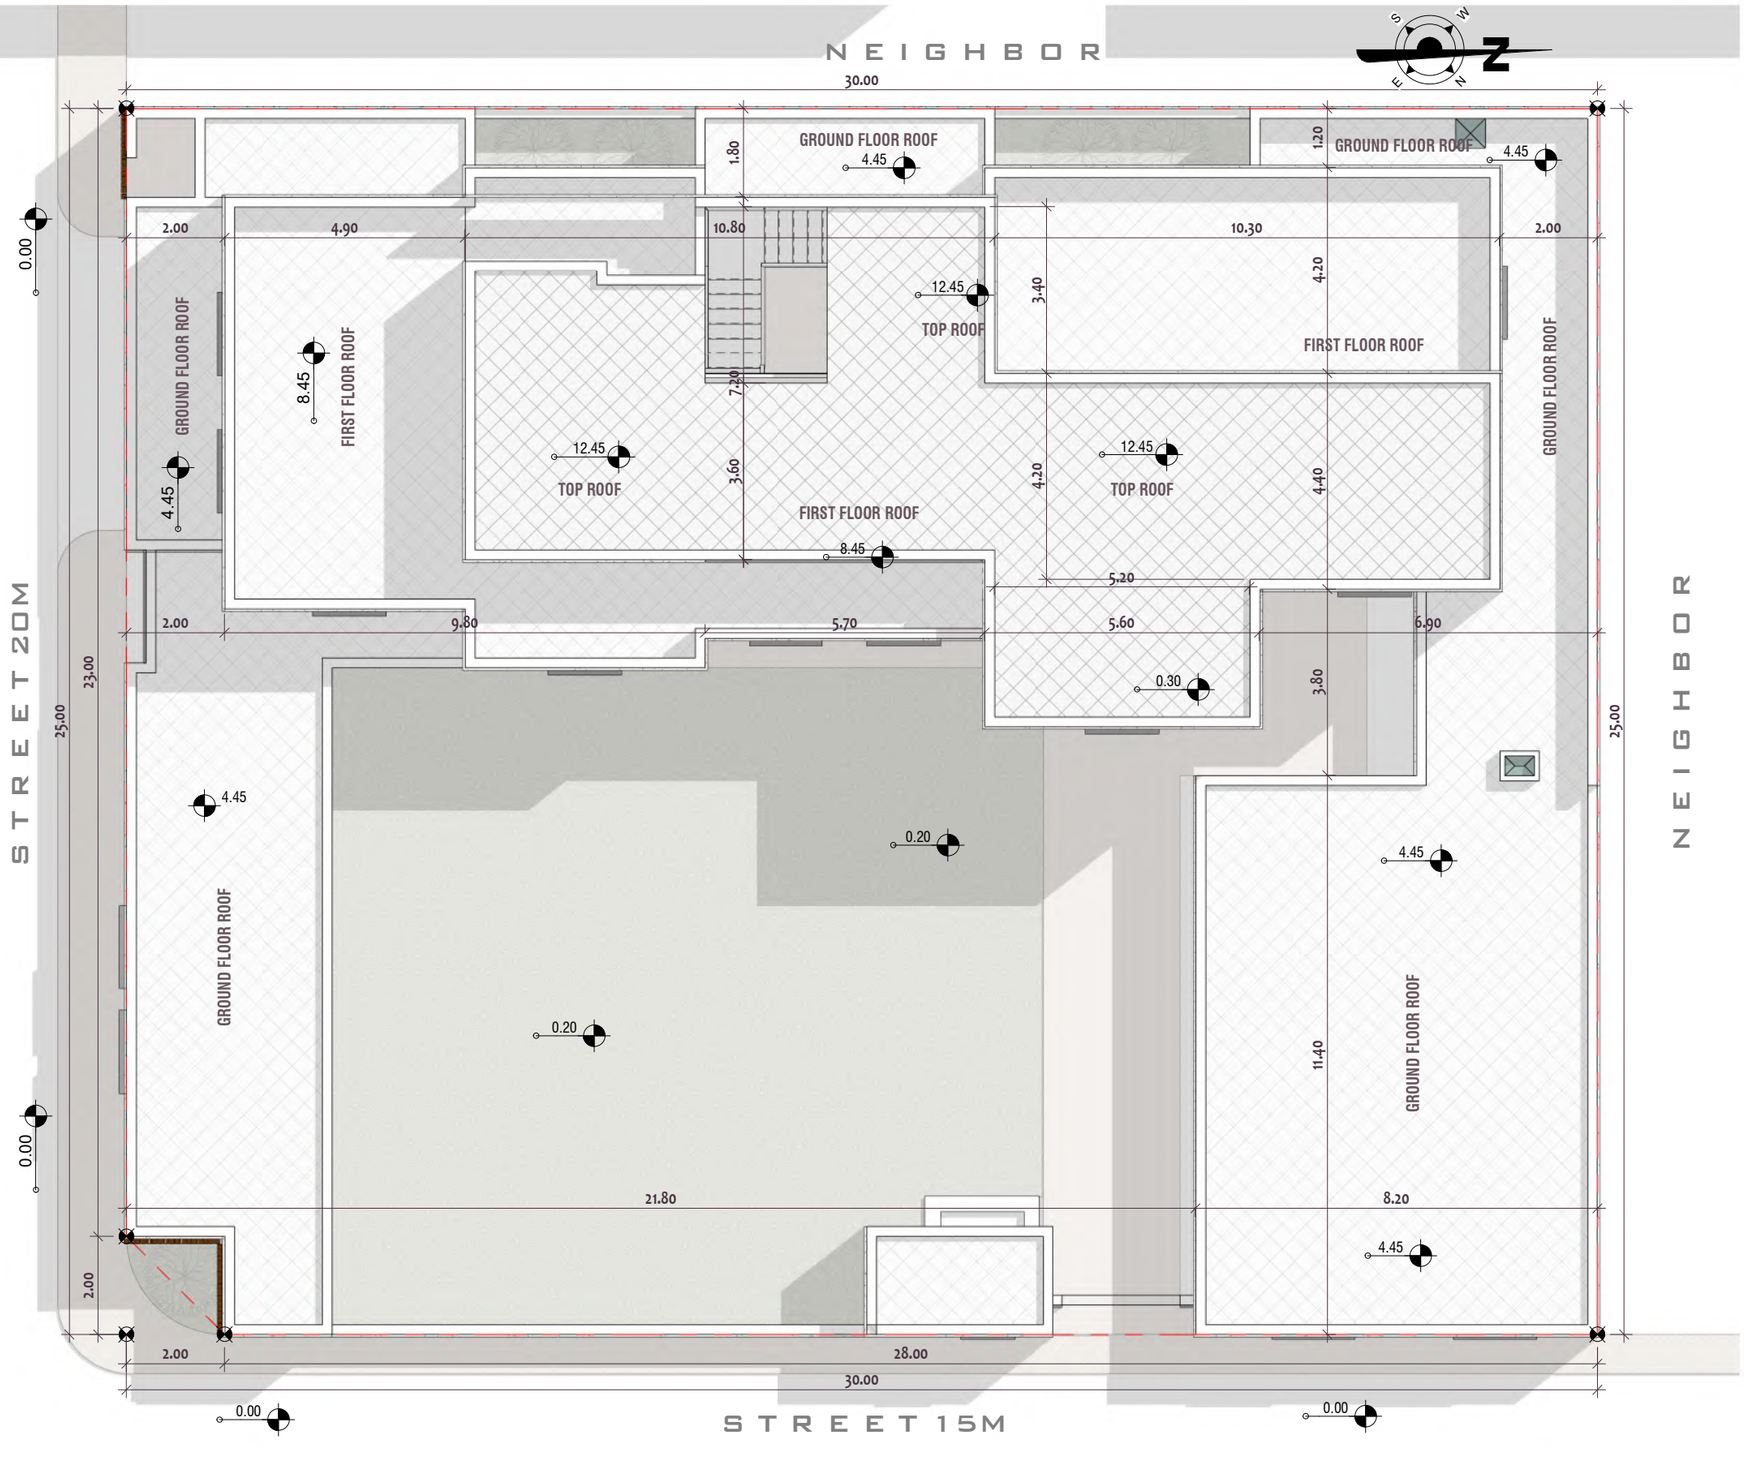

GENERAL NOTES:

1. ALL DIMENSION SHOWN HEREIN ARE ALL IN METERS, UNLESS OR OTHERWISE IT IS SPECIFIED

2. WINDOWS AND WINDOW SCREEN OPENING ON THE JOBSITE AND SUBMIT THE SHOP DRAWINGS PRIOR TO FABRICATION AND INSTALLTION.

3. ALL SHOP DRAWING, SAMPLES, CATALOG CUTOUTS, ETC. TO BE APPROVED BY THE ARCHITECT BEFORE FINAL EXECUTION.

4. REFER TO MECHANICAL, PLUMBING DRAWING FOR AN EXACT LOCATION AND SIZES OF ALL MECHANICAL ELEMENTS SHOWN ON CEILING AND ROOF PLANS.

5. LIGHTING FIXTURE TO BE COORDINATED WITH AN ARCHITECT.

6.ANY DISCREPANCY ON SITE AND ON SHOP DRAWINGS, REFER TO CONSULTING ARCHITECT.

7. FOR DOORS, WINDOWS AND ROOM FINISHING SCHEDULE REFER TO DRAWING NO.___

8. CONTRACTOR SHALL VERIFY ALL STRUCTURAL CONDITIONS AND DETAILS PRIOR TO FINAL EXECUTION AND TO ANY DEMOLITION.

9. FOR ALL PERMANENT STRUCTURAL ELEMENTS, REFER TO STRUCTURAL DRAWINGS.

10. MINIMUN PARKING SPACE IS 2.50M WIDTH AND 5.50M LENGTH.

11.

12. INSTALLATION OF ALL MECHANICAL, ELECTRICAL AND PLUMBING ELEMENTS SHALL BE REFER TO MANUFACTURER'S MANUAL.

13. OR UNLESS OTHERWISE BE SPECIFIED

THE INTERIOR DESIGN:

FOR THE FOLLOWING ITEMS:
-CEILING
-DOOR & WINDOW
-FINISHING
-TOILET (WALL TILLING)
-SKYLIGHT
-HANDRAILS

KEYPLAN:

OFFICIAL STAMP:

- [ ] FINAL
- [ ] FOR CONSTRUCTION
- [ ] AS-BUILT
- [ ] APPROVED AS NOTED
- [ ] FOR MUNICIPALITIES
- [ ] OTHERS

PROJECT:
فيلا سكنية

OWNER:
سعود محمد سعود المسعود

ALJEEL ARCHITECTS
Design - Project Management - Supervision
6071 King Abdulaziz.Rd- Riyadh - Saudi Arabia
Tel:+966-11-269-0811
WWW.ALJEEL-ARCH.COM

DRAWING TITLE: SITE PLAN

SHEET NO.: A104

SCALE: 1 : 110

DESIGNED BY:	APPROVED BY:	DRAWN BY:	DATE:
Arch. Saleh	Arch. Saleh	Utman	SEPT 2023
PROJECT NO.: Al-Jeel 213	STATUS: Initial Presentation	REVISION: ---	CODE:

7/14/2024 10:53:43 AM

C:\Users\Mohammed\ALJEEL ARCHITECTS Dropbox\design\Aljeel office Dropbox\Running Projects\213-فيلا سعود\Design\Arch\Rvt\VILLA SAUD UPDATE NEW FOR BAADIYA.rvt

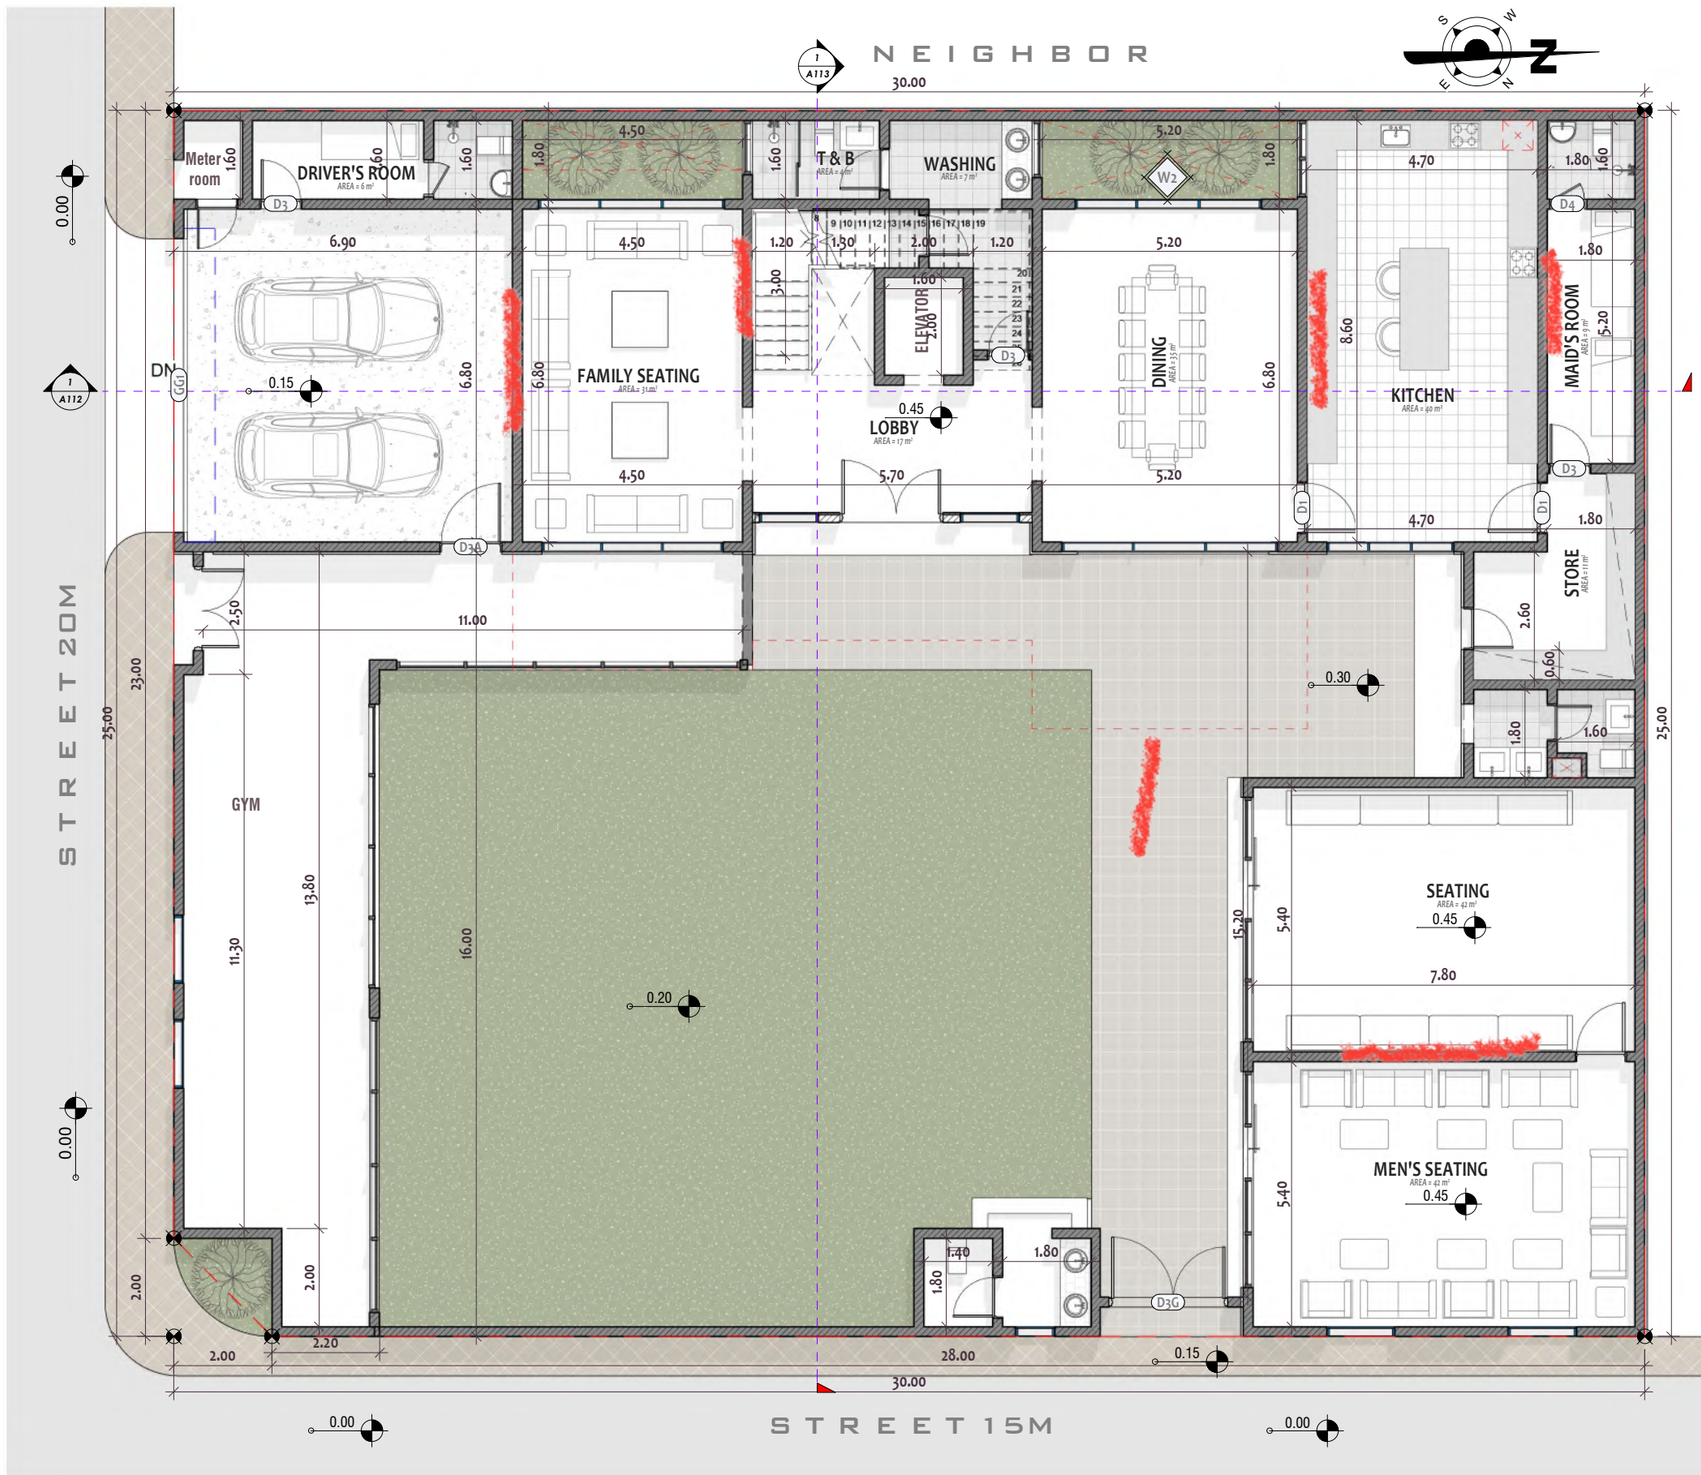

GENERAL NOTES:

1. ALL DIMENSION SHOWN HEREIN ARE ALL IN METERS, UNLESS OR OTHERWISE IT IS SPECIFIED

2. WINDOWS AND WINDOW SCREEN OPENING ON THE JOBSITE AND SUBMIT THE SHOP DRAWINGS PRIOR TO FABRICATION AND INSTALLTION.

3. ALL SHOP DRAWING, SAMPLES, CATALOG CUTOUTS, ETC. TO BE APPROVED BY THE ARCHITECT BEFORE FINAL EXECUTION.

4. REFER TO MECHANICAL, PLUMBING DRAWING FOR AN EXACT LOCATION AND SIZES OF ALL MECHANICAL ELEMENTS SHOWN ON CEILING AND ROOF PLANS.

5. LIGHTING FIXTURE TO BE COORDINATED WITH AN ARCHITECT.

6.ANY DISCREPANCY ON SITE AND ON SHOP DRAWINGS, REFER TO CONSULTING ARCHITECT.

7. FOR DOORS, WINDOWS AND ROOM FINISHING SCHEDULE REFER TO DRAWING NO.___

8. CONTRACTOR SHALL VERIFY ALL STRUCTURAL CONDITIONS AND DETAILS PRIOR TO FINAL EXECUTION AND TO ANY DEMOLITION.

9. FOR ALL PERMANENT STRUCTURAL ELEMENTS, REFER TO STRUCTURAL DRAWINGS.

10. MINIMUN PARKING SPACE IS 2.50M WIDTH AND 5.50M LENGTH.

11.

12. INSTALLATION OF ALL MECHANICAL, ELECTRICAL AND PLUMBING ELEMENTS SHALL BE REFER TO MANUFACTURER'S MANUAL.

13. OR UNLESS OTHERWISE BE SPECIFIED

THE INTERIOR DESIGN:

FOR THE FOLLOWING ITEMS:
-CEILING
-DOOR & WINDOW
-FINISHING
-TOILET (WALL TILLING)
-SKYLIGHT
-HANDRAILS

KEYPLAN:

OFFICIAL STAMP:

- [ ] FINAL
- [ ] FOR CONSTRUCTION
- [ ] AS-BUILT
- [ ] APPROVED AS NOTED
- [ ] FOR MUNICIPALITIES
- [ ] OTHERS

PROJECT:
فيلا سكنية

OWNER:
سعود محمد سعود المسعود

ALJEEL ARCHITECTS
Design - Project Management - Supervision
6071 King Abdulaziz.Rd- Riyadh - Saudi Arabia
Tel:+966-11-269-0811
WWW.ALJEEL-ARCH.COM

DRAWING TITLE: GROUND FLOOR PLAN

SHEET NO.: A105

SCALE: 1 : 110

DESIGNED BY:	APPROVED BY:	DRAWN BY:	DATE:
Arch. Saleh	Arch. Saleh	Utman	SEPT 2023
PROJECT NO.:	STATUS:	REVISION	CODE:
Al-Jeel 213	Initial Presentation	---	

7/14/2024 10:53:47 AM

C:\Users\Mohammed\ALJEEL ARCHITECTS Dropbox\design\Aljeel office Dropbox\Running Projects\213-فيلا سعود\Design\Arch\Rvt\VILLA SAUD UPDATE NEW FOR BAADIYA.rvt

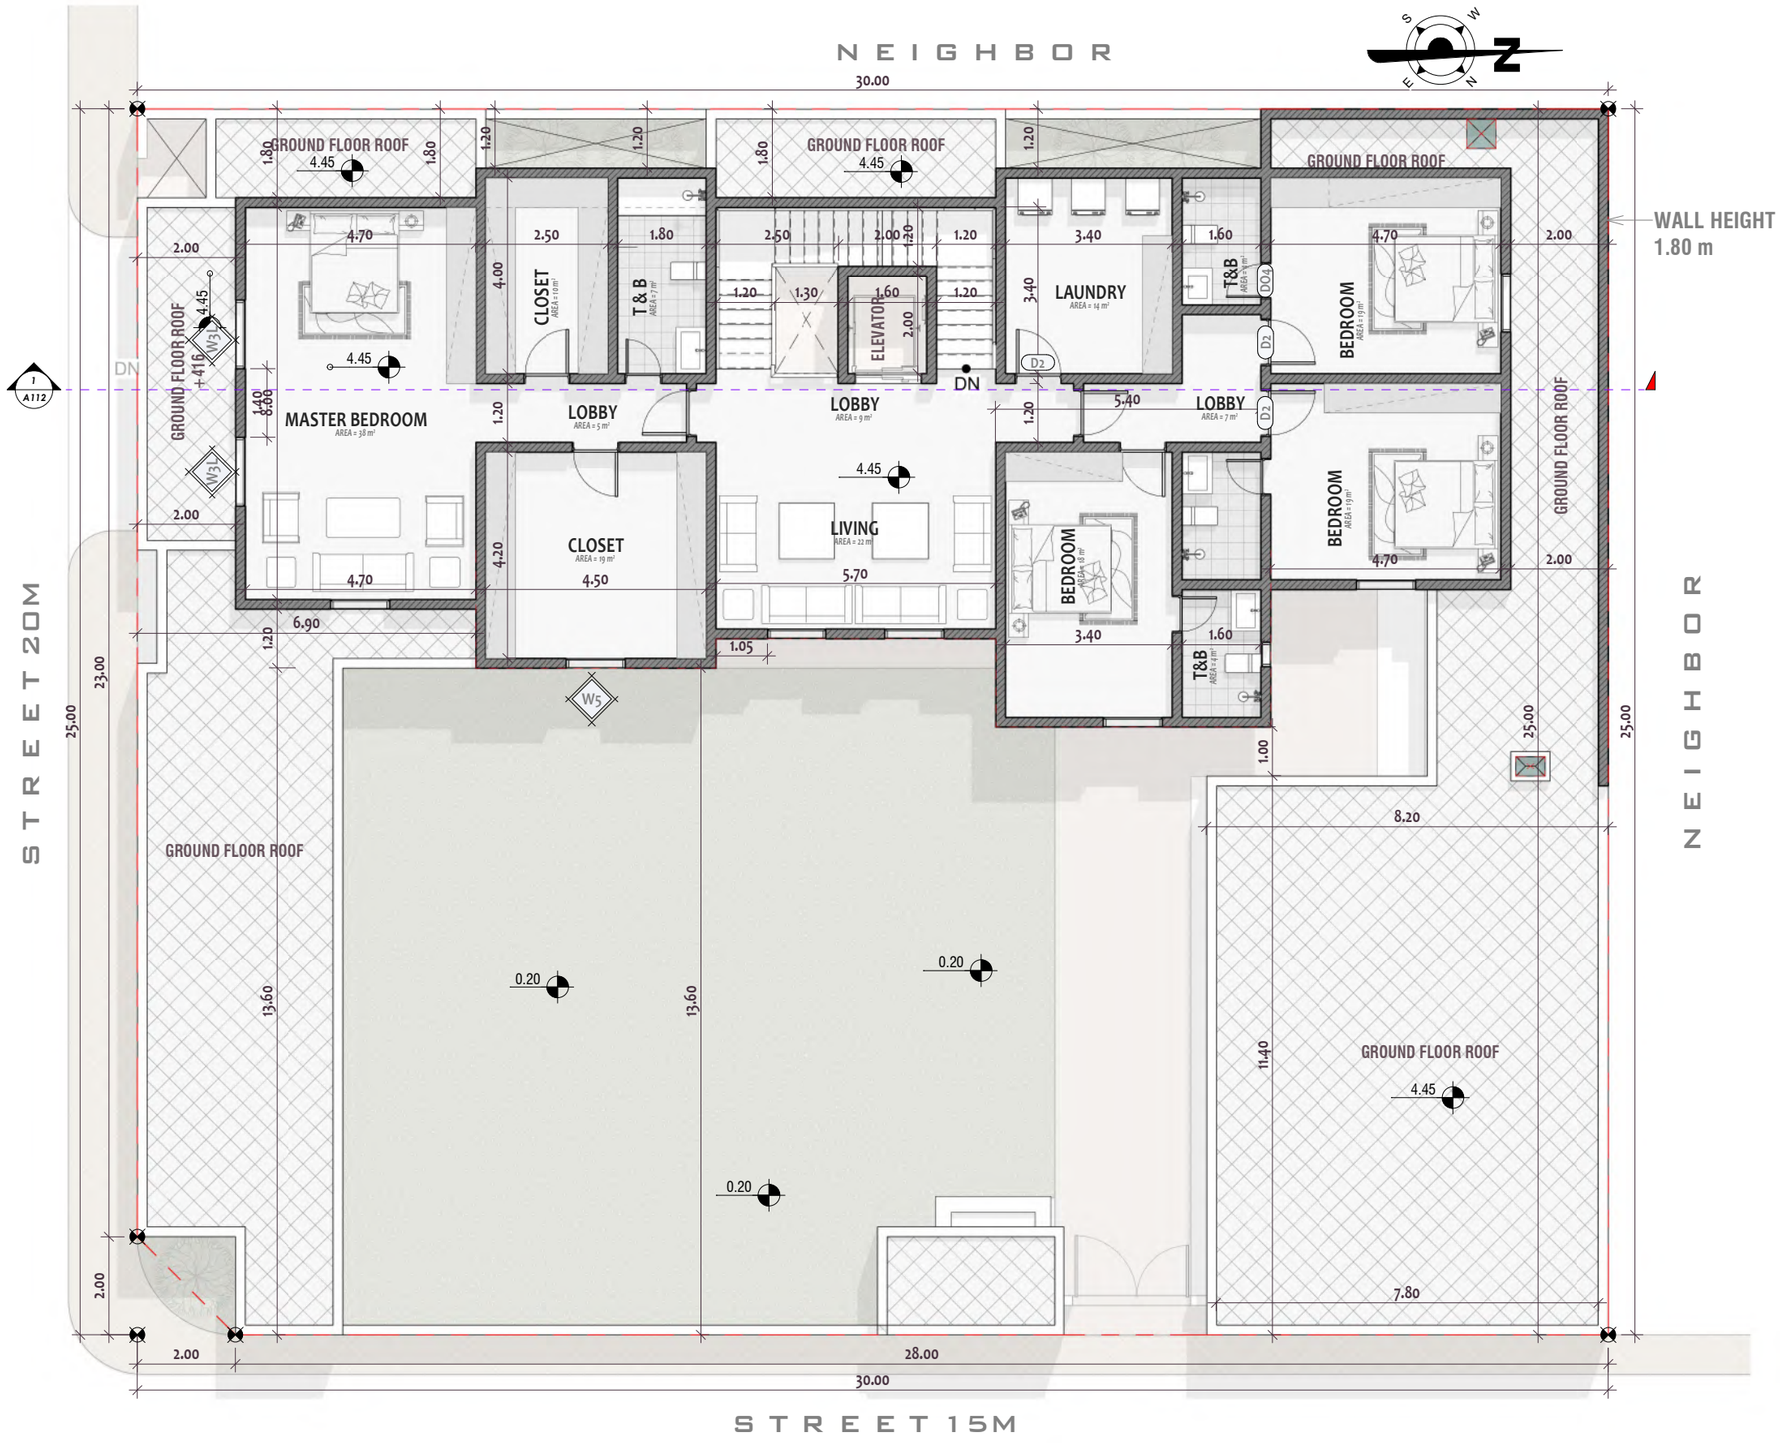

GENERAL NOTES:

1. ALL DIMENSION SHOWN HEREIN ARE ALL IN METERS, UNLESS OR OTHERWISE IT IS SPECIFIED

2. WINDOWS AND WINDOW SCREEN OPENING ON THE JOBSITE AND SUBMIT THE SHOP DRAWINGS PRIOR TO FABRICATION AND INSTALLTION.

3. ALL SHOP DRAWING, SAMPLES, CATALOG CUTOUTS, ETC. TO BE APPROVED BY THE ARCHITECT BEFORE FINAL EXECUTION.

4. REFER TO MECHANICAL, PLUMBING DRAWING FOR AN EXACT LOCATION AND SIZES OF ALL MECHANICAL ELEMENTS SHOWN ON CEILING AND ROOF PLANS.

5. LIGHTING FIXTURE TO BE COORDINATED WITH AN ARCHITECT.

6.ANY DISCREPANCY ON SITE AND ON SHOP DRAWINGS, REFER TO CONSULTING ARCHITECT.

7. FOR DOORS, WINDOWS AND ROOM FINISHING SCHEDULE REFER TO DRAWING NO.___

8. CONTRACTOR SHALL VERIFY ALL STRUCTURAL CONDITIONS AND DETAILS PRIOR TO FINAL EXECUTION AND TO ANY DEMOLITION.

9. FOR ALL PERMANENT STRUCTURAL ELEMENTS, REFER TO STRUCTURAL DRAWINGS.

10. MINIMUN PARKING SPACE IS 2.50M WIDTH AND 5.50M LENGTH.

11.

12. INSTALLATION OF ALL MECHANICAL, ELECTRICAL AND PLUMBING ELEMENTS SHALL BE REFER TO MANUFACTURER'S MANUAL.

13. OR UNLESS OTHERWISE BE SPECIFIED

THE INTERIOR DESIGN:
FOR THE FOLLOWING ITEMS:
-CEILING
-DOOR & WINDOW
-FINISHING
-TOILET (WALL TILLING)
-SKYLIGHT
-HANDRAILS

KEYPLAN:

OFFICIAL STAMP:

- [ ] FINAL
- [ ] FOR CONSTRUCTION
- [ ] AS-BUILT
- [ ] APPROVED AS NOTED
- [ ] FOR MUNICIPALITIES
- [ ] OTHERS

DISCIPLINE:
ARCHITECTURE

PROJECT:
فيلا سكنية

OWNER:
سعود محمد سعود المسعود

ALJEEL ARCHITECTS
Design - Project Management - Supervision
6071 King Abdulaziz.Rd- Riyadh - Saudi Arabia
Tel:+966-11-269-0811
WWW.ALJEEL-ARCH.COM

DRAWING TITLE: FIRST FLOOR PLAN

SHEET NO.: A106

SCALE: 1 : 110

DESIGNED BY:	APPROVED BY:	DRAWN BY:	DATE:
Arch. Saleh	Arch. Saleh	Utman	06/02/21

PROJECT NO.:	STATUS:	REVISION	CODE:
Al-Jeel 104	Initial Presentation	---	

7/14/2024 10:53:52 AM

C:\Users\Mohammed\ALJEEL ARCHITECTS Dropbox\design\Aljeel office Dropbox\Running Projects\213-فيلا سعود\Design\Arch\Rvt\VILLA SAUD UPDATE NEW FOR BAADIYA.rvt

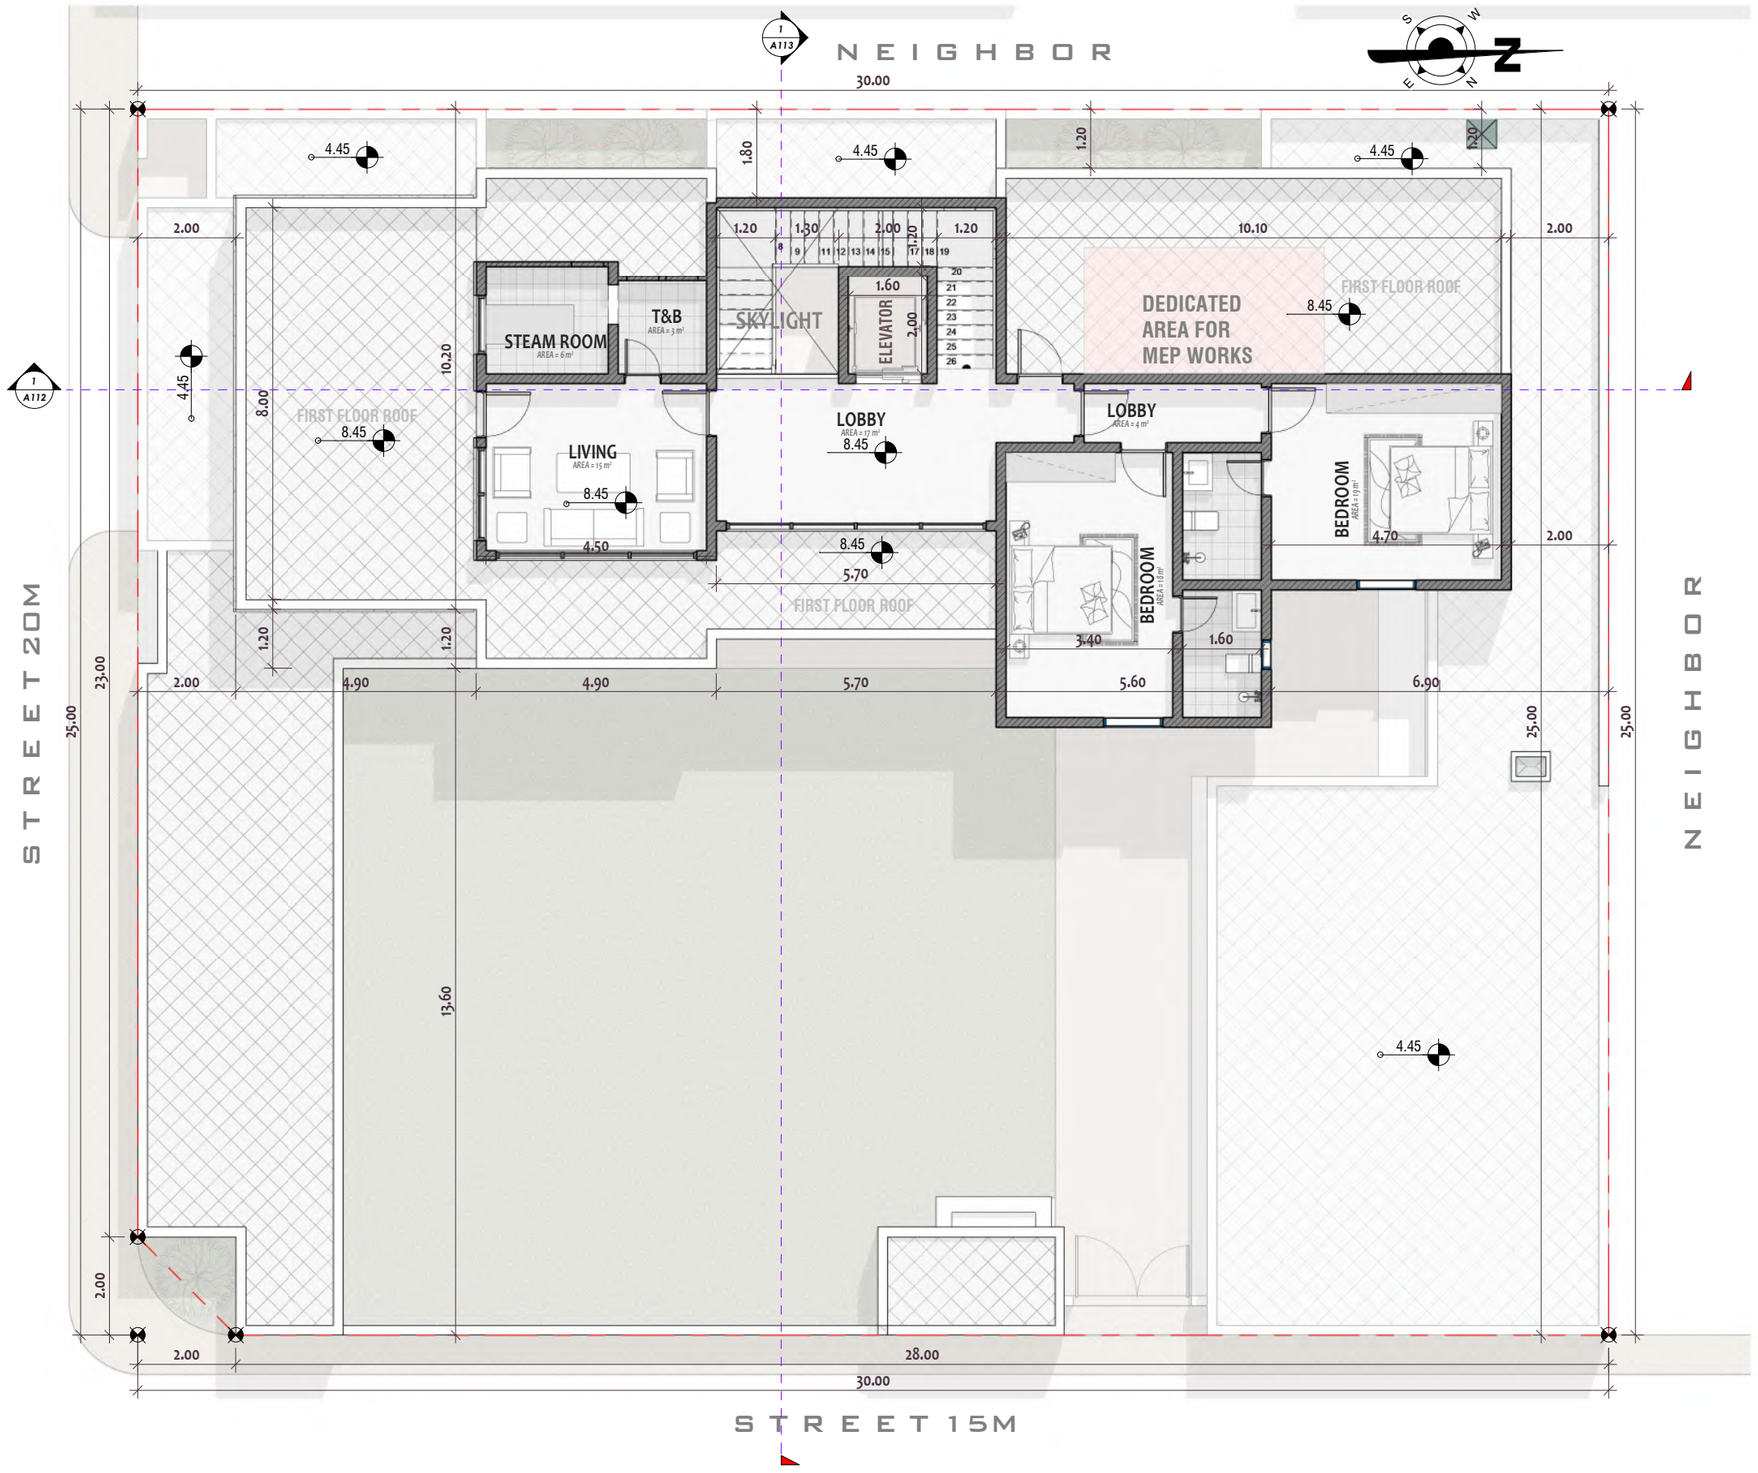

GENERAL NOTES:

1. ALL DIMENSION SHOWN HEREIN ARE ALL IN METERS, UNLESS OR OTHERWISE IT IS SPECIFIED

2. WINDOWS AND WINDOW SCREEN OPENING ON THE JOBSITE AND SUBMIT THE SHOP DRAWINGS PRIOR TO FABRICATION AND INSTALLTION.

3. ALL SHOP DRAWING, SAMPLES, CATALOG CUTOUTS, ETC. TO BE APPROVED BY THE ARCHITECT BEFORE FINAL EXECUTION.

4. REFER TO MECHANICAL, PLUMBING DRAWING FOR AN EXACT LOCATION AND SIZES OF ALL MECHANICAL ELEMENTS SHOWN ON CEILING AND ROOF PLANS.

5. LIGHTING FIXTURE TO BE COORDINATED WITH AN ARCHITECT.

6.ANY DISCREPANCY ON SITE AND ON SHOP DRAWINGS, REFER TO CONSULTING ARCHITECT.

7. FOR DOORS, WINDOWS AND ROOM FINISHING SCHEDULE REFER TO DRAWING NO.___

8. CONTRACTOR SHALL VERIFY ALL STRUCTURAL CONDITIONS AND DETAILS PRIOR TO FINAL EXECUTION AND TO ANY DEMOLITION.

9. FOR ALL PERMANENT STRUCTURAL ELEMENTS, REFER TO STRUCTURAL DRAWINGS.

10. MINIMUN PARKING SPACE IS 2.50M WIDTH AND 5.50M LENGTH.

11.

12. INSTALLATION OF ALL MECHANICAL, ELECTRICAL AND PLUMBING ELEMENTS SHALL BE REFER TO MANUFACTURER'S MANUAL.

13. OR UNLESS OTHERWISE BE SPECIFIED

THE INTERIOR DESIGN:
FOR THE FOLLOWING ITEMS:
-CEILING
-DOOR & WINDOW
-FINISHING
-TOILET (WALL TILLING)
-SKYLIGHT
-HANDRAILS

KEYPLAN:

OFFICIAL STAMP:

- [ ] FINAL
- [ ] FOR CONSTRUCTION
- [ ] AS-BUILT
- [ ] APPROVED AS NOTED
- [ ] FOR MUNICIPALITIES
- [ ] OTHERS

DISCIPLINE:
ARCHITECTURE

PROJECT:
فيلا سكنية

OWNER:
سعود محمد سعود المسعود

ALJEEL ARCHITECTS
Design - Project Management - Supervision
6071 King Abdulaziz.Rd- Riyadh - Saudi Arabia
Tel:+966-11-269-0811
WWW.ALJEEL-ARCH.COM

DRAWING TITLE: ROOF FLOOR PLAN

SHEET NO.: A107

SCALE: 1 : 110

DESIGNED BY:	APPROVED BY:	DRAWN BY:	DATE:
Arch. Saleh	Arch. Saleh	Utman	06/02/21

PROJECT NO.:	STATUS:	REVISION	CODE:
Al-Jeel 104	Initial Presentation	---	

7/14/2024 10:53:57 AM

C:\Users\Mohammed\ALJEEL ARCHITECTS Dropbox\design\Aljeel office Dropbox\Running Projects\213-فيلا سعود\Design\Arch\Rvt\VILLA SAUD UPDATE NEW FOR BAADIYA.rvt

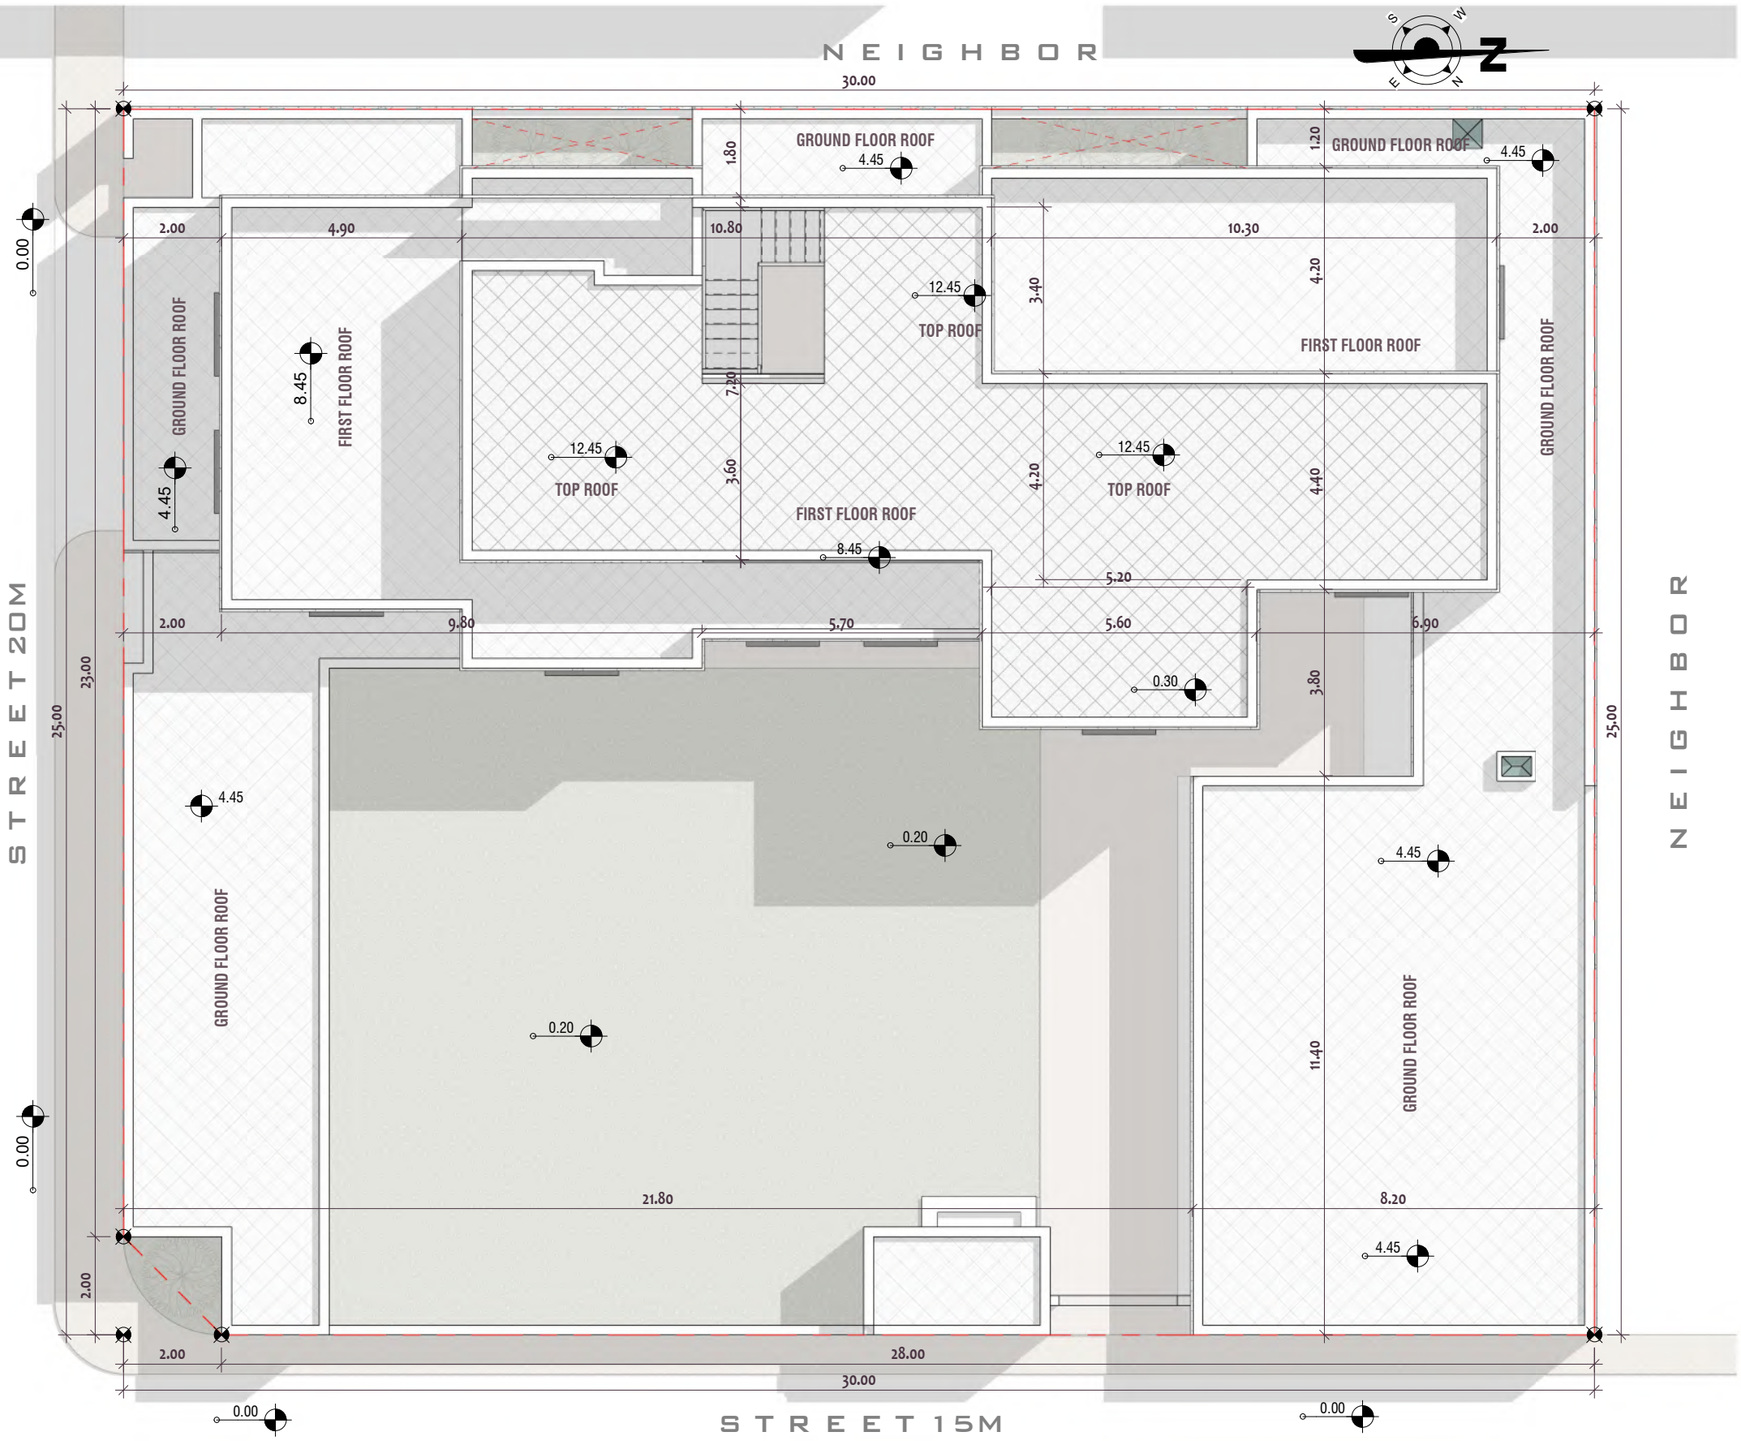

GENERAL NOTES:

1. ALL DIMENSION SHOWN HEREIN ARE ALL IN METERS, UNLESS OR OTHERWISE IT IS SPECIFIED

2. WINDOWS AND WINDOW SCREEN OPENING ON THE JOBSITE AND SUBMIT THE SHOP DRAWINGS PRIOR TO FABRICATION AND INSTALLTION.

3. ALL SHOP DRAWING, SAMPLES, CATALOG CUTOUTS, ETC. TO BE APPROVED BY THE ARCHITECT BEFORE FINAL EXECUTION.

4. REFER TO MECHANICAL, PLUMBING DRAWING FOR AN EXACT LOCATION AND SIZES OF ALL MECHANICAL ELEMENTS SHOWN ON CEILING AND ROOF PLANS.

5. LIGHTING FIXTURE TO BE COORDINATED WITH AN ARCHITECT.

6.ANY DISCREPANCY ON SITE AND ON SHOP DRAWINGS, REFER TO CONSULTING ARCHITECT.

7. FOR DOORS, WINDOWS AND ROOM FINISHING SCHEDULE REFER TO DRAWING NO.___

8. CONTRACTOR SHALL VERIFY ALL STRUCTURAL CONDITIONS AND DETAILS PRIOR TO FINAL EXECUTION AND TO ANY DEMOLITION.

9. FOR ALL PERMANENT STRUCTURAL ELEMENTS, REFER TO STRUCTURAL DRAWINGS.

10. MINIMUN PARKING SPACE IS 2.50M WIDTH AND 5.50M LENGTH.

11.

12. INSTALLATION OF ALL MECHANICAL, ELECTRICAL AND PLUMBING ELEMENTS SHALL BE REFER TO MANUFACTURER'S MANUAL.

13. OR UNLESS OTHERWISE BE SPECIFIED

THE INTERIOR DESIGN:
FOR THE FOLLOWING ITEMS:
-CEILING
-DOOR & WINDOW
-FINISHING
-TOILET (WALL TILLING)
-SKYLIGHT
-HANDRAILS

KEYPLAN:

OFFICIAL STAMP:

- [ ] FINAL
- [ ] FOR CONSTRUCTION
- [ ] AS-BUILT
- [ ] APPROVED AS NOTED
- [ ] FOR MUNICIPALITIES
- [ ] OTHERS

DISCIPLINE:
ARCHITECTURE

PROJECT:
فيلا سكنية

OWNER:
سعود محمد سعود المسعود

ALJEEL ARCHITECTS
Design - Project Management - Supervision
6071 King Abdulaziz.Rd- Riyadh - Saudi Arabia
Tel:+966-11-269-0811
WWW.ALJEEL-ARCH.COM

DRAWING TITLE: UPPER ROOF FLOOR PLAN

SHEET NO.: A0107

SCALE: 1 : 110

DESIGNED BY:	APPROVED BY:	DRAWN BY:	DATE:
Arch. Saleh	Arch. Saleh	Utman	05/20/24
PROJECT NO.:	STATUS:	REVISION	CODE:
Al-Jeel 104	Initial Presentation	---	

7/14/2024 10:54:05 AM

C:\Users\Mohammed\ALJEEL ARCHITECTS Dropbox\design\Aljeel office Dropbox\Running Projects\213-فيلا سعود\Design\Arch\Rvt\VILLA SAUD UPDATE NEW FOR BAADIYA.rvt

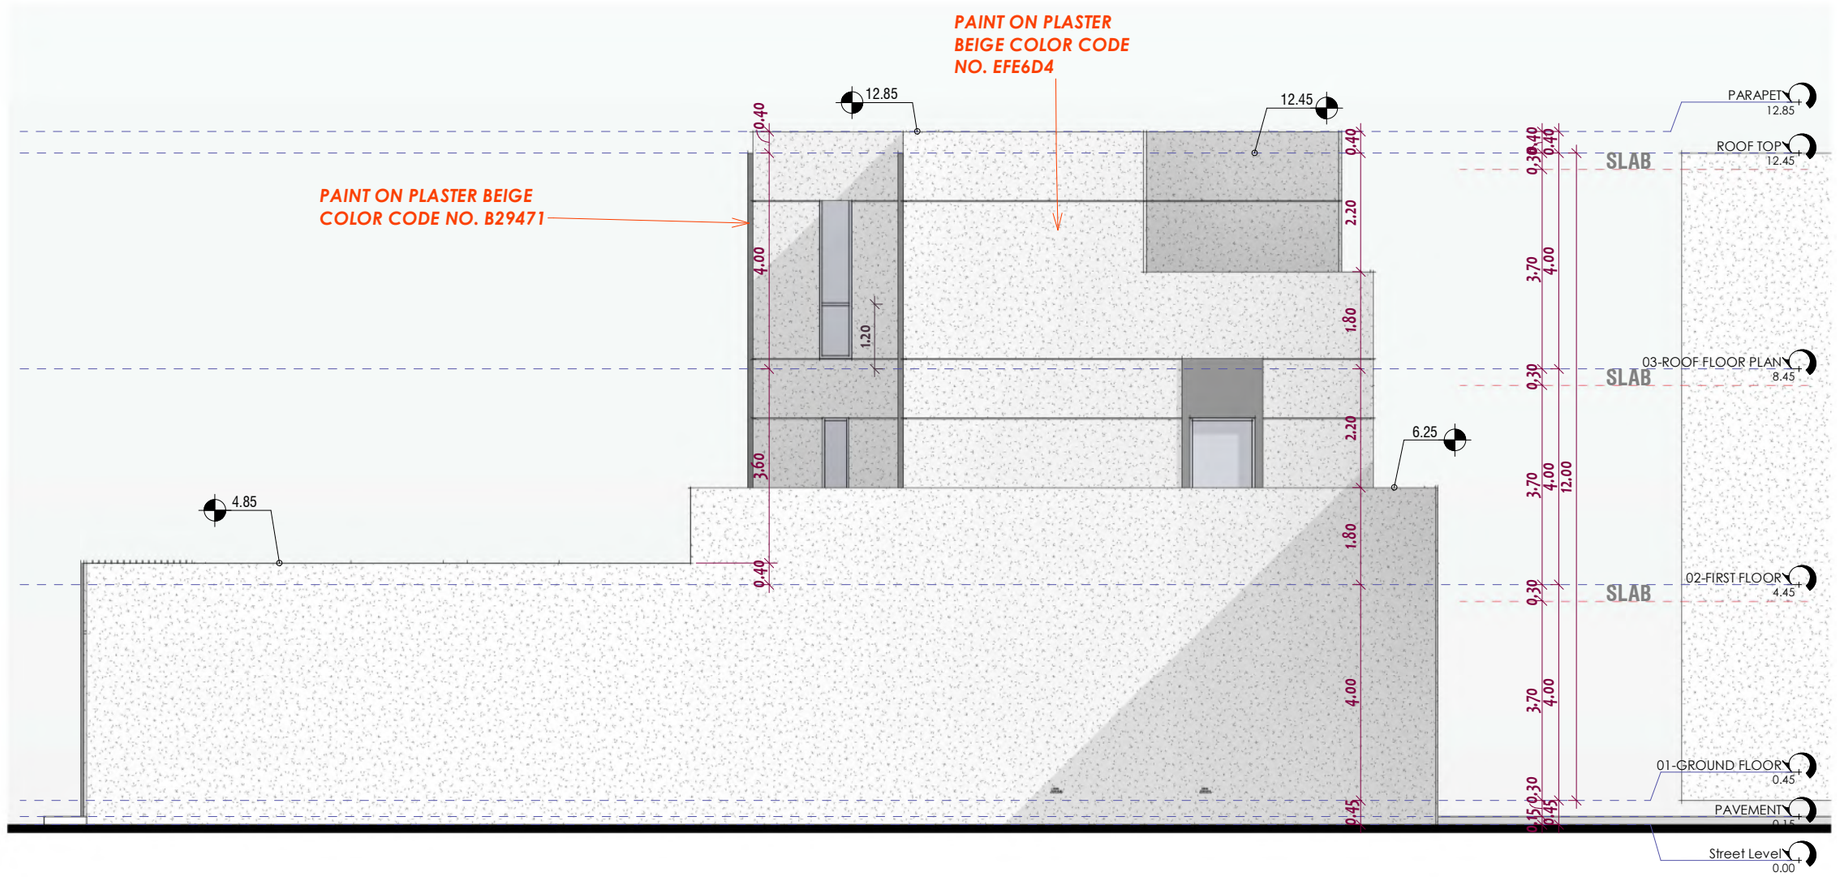

GENERAL NOTES:

1. ALL DIMENSION SHOWN HEREIN ARE ALL IN METERS, UNLESS OR OTHERWISE IT IS SPECIFIED

2. WINDOWS AND WINDOW SCREEN OPENING ON THE JOBSITE AND SUBMIT THE SHOP DRAWINGS PRIOR TO FABRICATION AND INSTALLTION.

3. ALL SHOP DRAWING, SAMPLES, CATALOG CUTOUTS, ETC. TO BE APPROVED BY THE ARCHITECT BEFORE FINAL EXECUTION.

4. REFER TO MECHANICAL, PLUMBING DRAWING FOR AN EXACT LOCATION AND SIZES OF ALL MECHANICAL ELEMENTS SHOWN ON CEILING AND ROOF PLANS.

5. LIGHTING FIXTURE TO BE COORDINATED WITH AN ARCHITECT.

6.ANY DISCREPANCY ON SITE AND ON SHOP DRAWINGS, REFER TO CONSULTING ARCHITECT.

7. FOR DOORS, WINDOWS AND ROOM FINISHING SCHEDULE REFER TO DRAWING NO.___

8. CONTRACTOR SHALL VERIFY ALL STRUCTURAL CONDITIONS AND DETAILS PRIOR TO FINAL EXECUTION AND TO ANY DEMOLITION.

9. FOR ALL PERMANENT STRUCTURAL ELEMENTS, REFER TO STRUCTURAL DRAWINGS.

10. MINIMUN PARKING SPACE IS 2.50M WIDTH AND 5.50M LENGTH.

11.

12. INSTALLATION OF ALL MECHANICAL, ELECTRICAL AND PLUMBING ELEMENTS SHALL BE REFER TO MANUFACTURER'S MANUAL.

13. OR UNLESS OTHERWISE BE SPECIFIED

THE INTERIOR DESIGN:
FOR THE FOLLOWING ITEMS:
-CEILING
-DOOR & WINDOW
-FINISHING
-TOILET (WALL TILLING)
-SKYLIGHT
-HANDRAILS

KEYPLAN:

OFFICIAL STAMP:

☐ FINAL
☐ FOR CONSTRUCTION
☐ AS-BUILT
☐ APPROVED AS NOTED
☐ FOR MUNICIPALITIES
☐ OTHERS

DISCIPLINE:
ARCHITECTURE

PROJECT:
فيلا سكنية

OWNER:
سعود محمد سعود المسعود

ALJEEL ARCHITECTS
Design - Project Management - Supervision
6071 King Abdulaziz.Rd- Riyadh - Saudi Arabia
Tel:+966-11-269-0811
WWW.ALJEEL-ARCH.COM

DRAWING TITLE:
EAST ELEVATION

SHEET NO.: A108
SCALE: 1 : 100

DESIGNED BY:	APPROVED BY:	DRAWN BY:	DATE:
Arch. Saleh	Arch. Saleh	Utman	06/02/21
PROJECT NO.:	STATUS:	REVISION	CODE:
Al-Jeel 104	Initial Presentation	---	

7/14/2024 10:55:01 AM

C:\Users\Mohammed\ALJEEL ARCHITECTS Dropbox\design\Aljeel office Dropbox\Running Projects\213-فيلا سعود\Design\Arch\Rvt\VILLA SAUD UPDATE NEW FOR BAADIYA.rvt

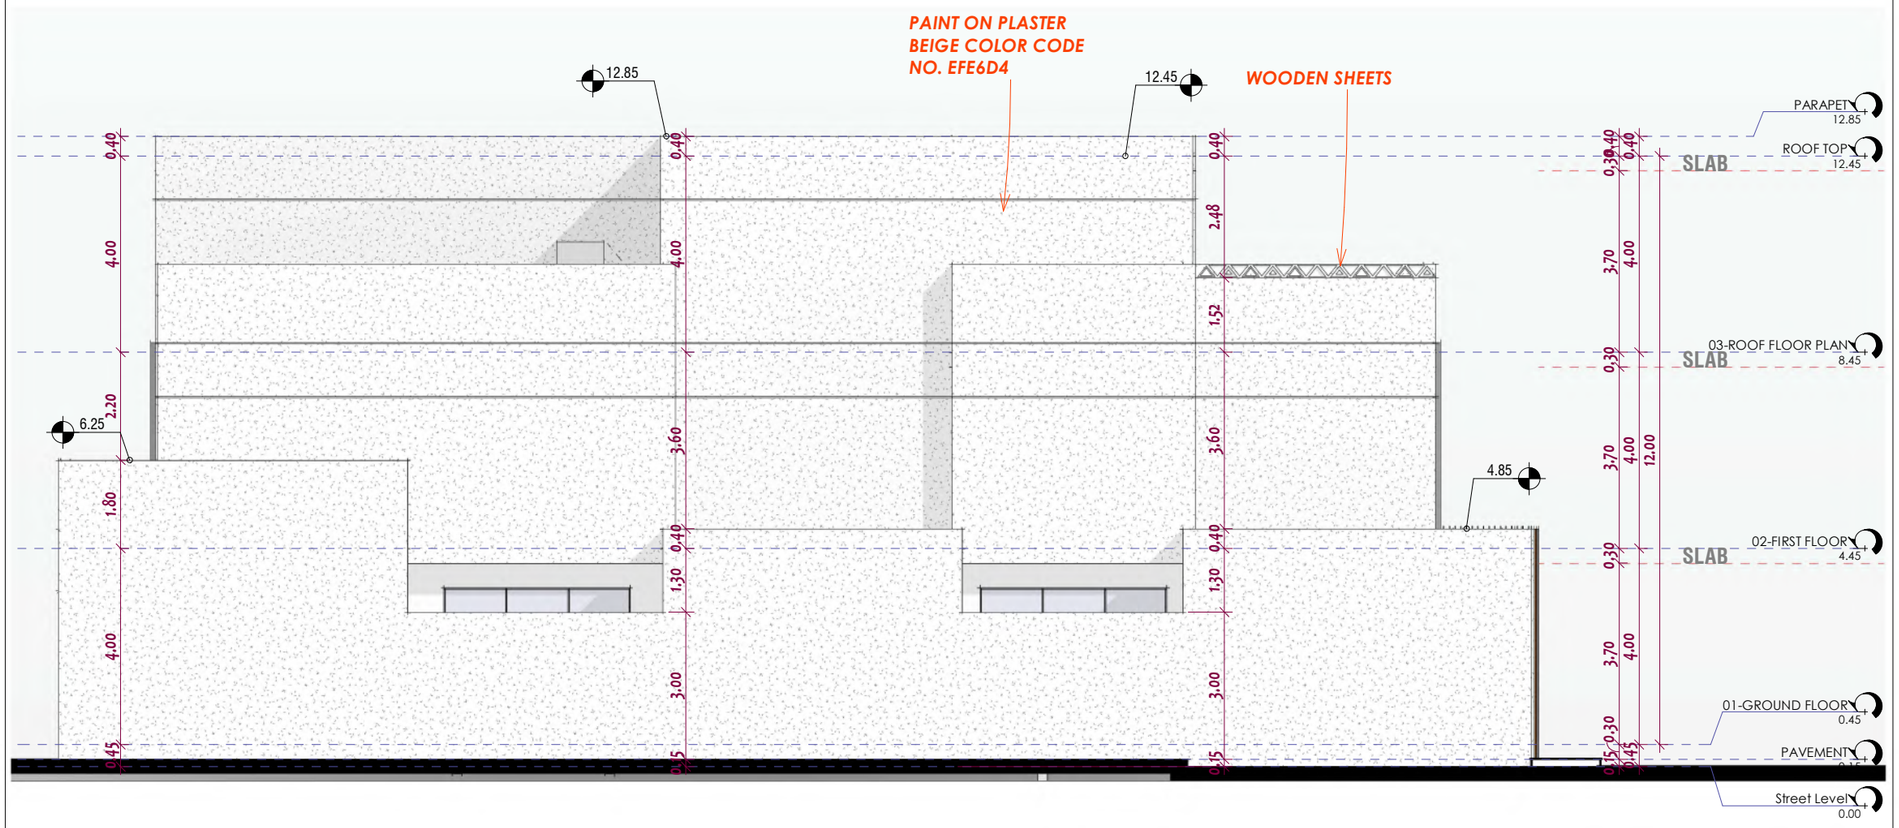

GENERAL NOTES:

1. ALL DIMENSION SHOWN HEREIN ARE ALL IN METERS, UNLESS OR OTHERWISE IT IS SPECIFIED

2. WINDOWS AND WINDOW SCREEN OPENING ON THE JOBSITE AND SUBMIT THE SHOP DRAWINGS PRIOR TO FABRICATION AND INSTALLTION.

3. ALL SHOP DRAWING, SAMPLES, CATALOG CUTOUTS, ETC. TO BE APPROVED BY THE ARCHITECT BEFORE FINAL EXECUTION.

4. REFER TO MECHANICAL, PLUMBING DRAWING FOR AN EXACT LOCATION AND SIZES OF ALL MECHANICAL ELEMENTS SHOWN ON CEILING AND ROOF PLANS.

5. LIGHTING FIXTURE TO BE COORDINATED WITH AN ARCHITECT.

6.ANY DISCREPANCY ON SITE AND ON SHOP DRAWINGS, REFER TO CONSULTING ARCHITECT.

7. FOR DOORS, WINDOWS AND ROOM FINISHING SCHEDULE REFER TO DRAWING NO.___

8. CONTRACTOR SHALL VERIFY ALL STRUCTURAL CONDITIONS AND DETAILS PRIOR TO FINAL EXECUTION AND TO ANY DEMOLITION.

9. FOR ALL PERMANENT STRUCTURAL ELEMENTS, REFER TO STRUCTURAL DRAWINGS.

10. MINIMUN PARKING SPACE IS 2.50M WIDTH AND 5.50M LENGTH.

11.

12. INSTALLATION OF ALL MECHANICAL, ELECTRICAL AND PLUMBING ELEMENTS SHALL BE REFER TO MANUFACTURER'S MANUAL.

13. OR UNLESS OTHERWISE BE SPECIFIED

THE INTERIOR DESIGN:
FOR THE FOLLOWING ITEMS:
-CEILING
-DOOR & WINDOW
-FINISHING
-TOILET (WALL TILLING)
-SKYLIGHT
-HANDRAILS

KEYPLAN:

OFFICIAL STAMP:

- [ ] FINAL
- [ ] FOR CONSTRUCTION
- [ ] AS-BUILT
- [ ] APPROVED AS NOTED
- [ ] FOR MUNICIPALITIES
- [ ] OTHERS

DISCIPLINE:
A R C H I T E C T U R E

PROJECT:
فيلا سكنية

OWNER:
سعود محمد سعود المسعود

ALJEEL ARCHITECTS
Design - Project Management - Supervision
6071 King Abdulaziz.Rd- Riyadh - Saudi Arabia
Tel:+966-11-269-0811
WWW.ALJEEL-ARCH.COM

DRAWING TITLE:
NORTH ELEVATION

SHEET NO.: A109
SCALE: 1 : 110

DESIGNED BY:	APPROVED BY:	DRAWN BY:	DATE:
Arch. Saleh	Arch. Saleh	Utman	06/02/21
PROJECT NO.:	STATUS:	REVISION	CODE:
Al-Jeel 104	Initial Presentation	---	

7/14/2024 10:55:09 AM

C:\Users\Mohammed\ALJEEL ARCHITECTS Dropbox\design\Aljeel office Dropbox\Running Projects\213-فيلا سعود\Design\Arch\Rvt\VILLA SAUD UPDATE NEW FOR BAADIYA.rvt

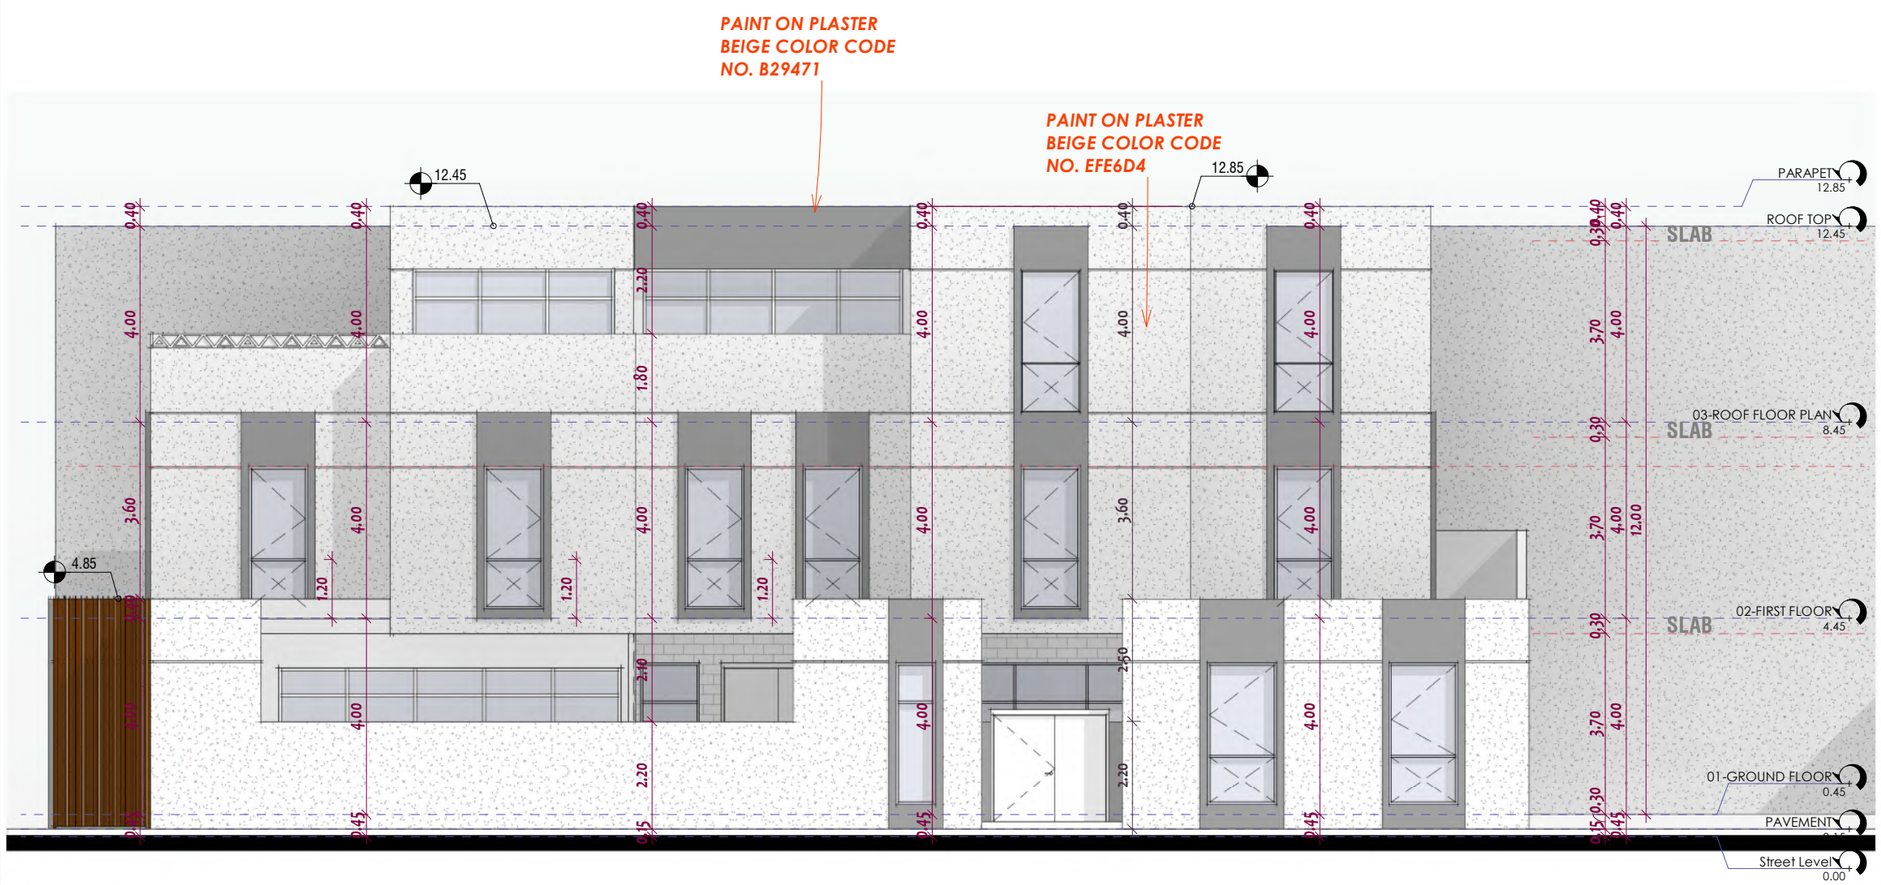

GENERAL NOTES:

1. ALL DIMENSION SHOWN HEREIN ARE ALL IN METERS, UNLESS OR OTHERWISE IT IS SPECIFIED

2. WINDOWS AND WINDOW SCREEN OPENING ON THE JOBSITE AND SUBMIT THE SHOP DRAWINGS PRIOR TO FABRICATION AND INSTALLTION.

3. ALL SHOP DRAWING, SAMPLES, CATALOG CUTOUTS, ETC. TO BE APPROVED BY THE ARCHITECT BEFORE FINAL EXECUTION.

4. REFER TO MECHANICAL, PLUMBING DRAWING FOR AN EXACT LOCATION AND SIZES OF ALL MECHANICAL ELEMENTS SHOWN ON CEILING AND ROOF PLANS.

5. LIGHTING FIXTURE TO BE COORDINATED WITH AN ARCHITECT.

6.ANY DISCREPANCY ON SITE AND ON SHOP DRAWINGS, REFER TO CONSULTING ARCHITECT.

7. FOR DOORS, WINDOWS AND ROOM FINISHING SCHEDULE REFER TO DRAWING NO.___

8. CONTRACTOR SHALL VERIFY ALL STRUCTURAL CONDITIONS AND DETAILS PRIOR TO FINAL EXECUTION AND TO ANY DEMOLITION.

9. FOR ALL PERMANENT STRUCTURAL ELEMENTS, REFER TO STRUCTURAL DRAWINGS.

10. MINIMUN PARKING SPACE IS 2.50M WIDTH AND 5.50M LENGTH.

11.

12. INSTALLATION OF ALL MECHANICAL, ELECTRICAL AND PLUMBING ELEMENTS SHALL BE REFER TO MANUFACTURER'S MANUAL.

13. OR UNLESS OTHERWISE BE SPECIFIED

THE INTERIOR DESIGN:
FOR THE FOLLOWING ITEMS:
-CEILING
-DOOR & WINDOW
-FINISHING
-TOILET (WALL TILLING)
-SKYLIGHT
-HANDRAILS

KEYPLAN:

OFFICIAL STAMP:

- [ ] FINAL
- [ ] FOR CONSTRUCTION
- [ ] AS-BUILT
- [ ] APPROVED AS NOTED
- [ ] FOR MUNICIPALITIES
- [ ] OTHERS

DISCIPLINE:
ARCHITECTURE

PROJECT:
فيلا سكنية

OWNER:
سعود محمد سعود المسعود

ALJEEL ARCHITECTS
Design - Project Management - Supervision
6071 King Abdulaziz.Rd- Riyadh - Saudi Arabia
Tel:+966-11-269-0811
WWW.ALJEEL-ARCH.COM

DRAWING TITLE:
SOUTH ELEVATION

SHEET NO.: A110
SCALE: 1 : 110

DESIGNED BY:	APPROVED BY:	DRAWN BY:	DATE:
Arch. Saleh	Arch. Saleh	Utman	06/02/21
PROJECT NO.:	**STATUS:**	**REVISION**	**CODE:**
Al-Jeel 104	Initial Presentation	---	

7/14/2024 10:55:18 AM

C:\Users\Mohammed\ALJEEL ARCHITECTS Dropbox\design\Aljeel office Dropbox\Running Projects\213-فيلا سعود\Design\Arch\Rvt\VILLA SAUD UPDATE NEW FOR BAADIYA.rvt

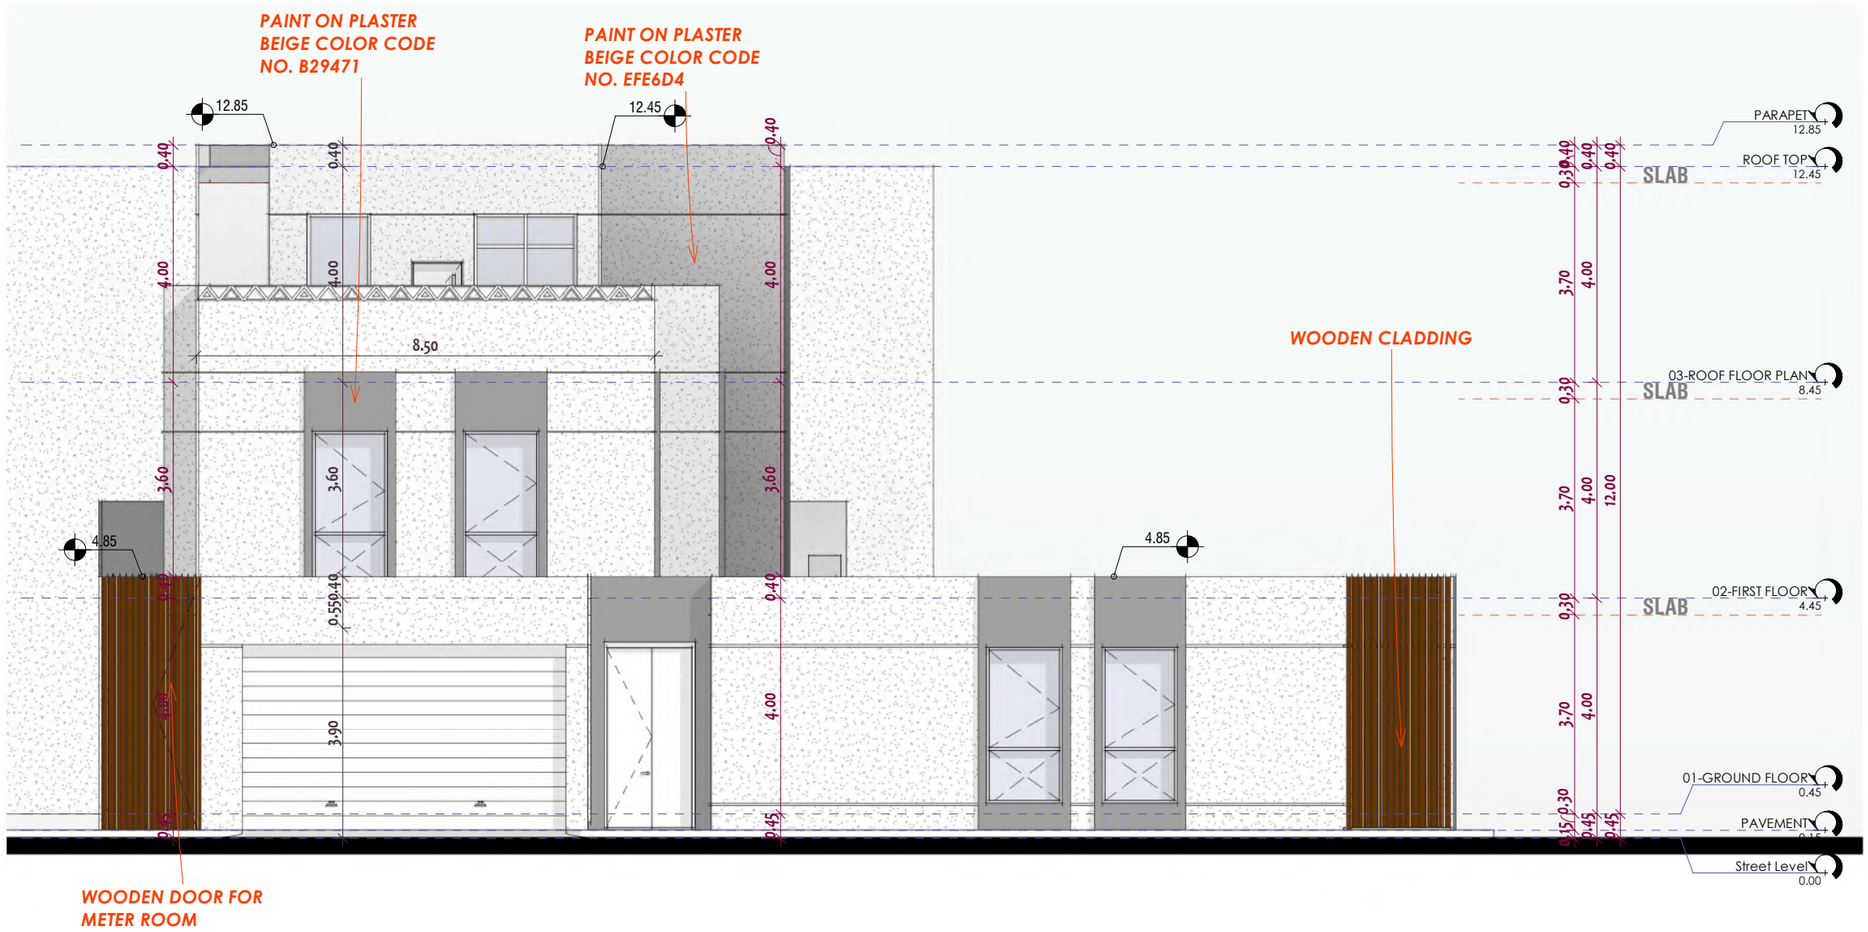

GENERAL NOTES:

1. ALL DIMENSION SHOWN HEREIN ARE ALL IN METERS, UNLESS OR OTHERWISE IT IS SPECIFIED

2. WINDOWS AND WINDOW SCREEN OPENING ON THE JOBSITE AND SUBMIT THE SHOP DRAWINGS PRIOR TO FABRICATION AND INSTALLTION.

3. ALL SHOP DRAWING, SAMPLES, CATALOG CUTOUTS, ETC. TO BE APPROVED BY THE ARCHITECT BEFORE FINAL EXECUTION.

4. REFER TO MECHANICAL, PLUMBING DRAWING FOR AN EXACT LOCATION AND SIZES OF ALL MECHANICAL ELEMENTS SHOWN ON CEILING AND ROOF PLANS.

5. LIGHTING FIXTURE TO BE COORDINATED WITH AN ARCHITECT.

6.ANY DISCREPANCY ON SITE AND ON SHOP DRAWINGS, REFER TO CONSULTING ARCHITECT.

7. FOR DOORS, WINDOWS AND ROOM FINISHING SCHEDULE REFER TO DRAWING NO.___

8. CONTRACTOR SHALL VERIFY ALL STRUCTURAL CONDITIONS AND DETAILS PRIOR TO FINAL EXECUTION AND TO ANY DEMOLITION.

9. FOR ALL PERMANENT STRUCTURAL ELEMENTS, REFER TO STRUCTURAL DRAWINGS.

10. MINIMUN PARKING SPACE IS 2.50M WIDTH AND 5.50M LENGTH.

11.

12. INSTALLATION OF ALL MECHANICAL, ELECTRICAL AND PLUMBING ELEMENTS SHALL BE REFER TO MANUFACTURER'S MANUAL.

13. OR UNLESS OTHERWISE BE SPECIFIED

THE INTERIOR DESIGN:
FOR THE FOLLOWING ITEMS:
-CEILING
-DOOR & WINDOW
-FINISHING
-TOILET (WALL TILLING)
-SKYLIGHT
-HANDRAILS

KEYPLAN:

OFFICIAL STAMP:

- [ ] FINAL
- [ ] FOR CONSTRUCTION
- [ ] AS-BUILT
- [ ] APPROVED AS NOTED
- [ ] FOR MUNICIPALITIES
- [ ] OTHERS

DISCIPLINE:
A R C H I T E C T U R E

PROJECT:
فيلا سكنية

OWNER:
سعود محمد سعود المسعود

ALJEEL ARCHITECTS
Design - Project Management - Supervision
6071 King Abdulaziz.Rd- Riyadh - Saudi Arabia
Tel:+966-11-269-0811
WWW.ALJEEL-ARCH.COM

DRAWING TITLE:
WEST ELEVATION

SHEET NO.: A111
SCALE: 1 : 100

DESIGNED BY:	APPROVED BY:	DRAWN BY:	DATE:
Arch. Saleh	Arch. Saleh	Utman	06/02/21
PROJECT NO.:	**STATUS:**	**REVISION**	**CODE:**
Al-Jeel 104	Initial Presentation	---	

7/14/2024 10:55:26 AM

C:\Users\Mohammed\ALJEEL ARCHITECTS Dropbox\design\Aljeel office Dropbox\Running Projects\213-فيلا سعود\Design\Arch\Rvt\VILLA SAUD UPDATE NEW FOR BAADIYA.rvt

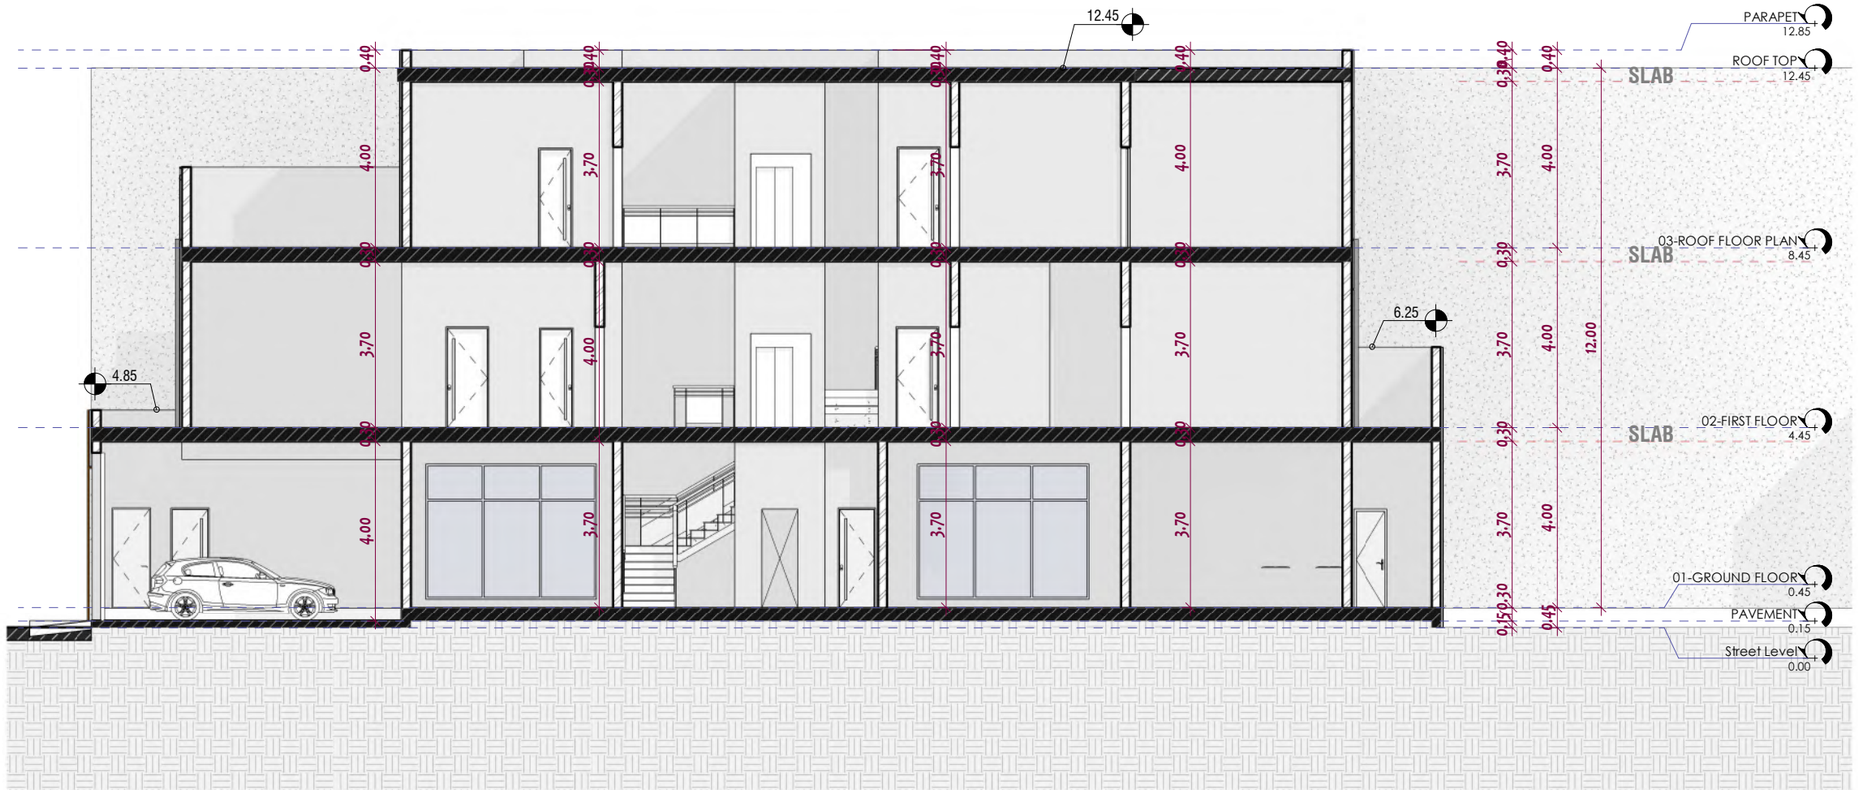

GENERAL NOTES:

1. ALL DIMENSION SHOWN HEREIN ARE ALL IN METERS, UNLESS OR OTHERWISE IT IS SPECIFIED

2. WINDOWS AND WINDOW SCREEN OPENING ON THE JOBSITE AND SUBMIT THE SHOP DRAWINGS PRIOR TO FABRICATION AND INSTALLTION.

3. ALL SHOP DRAWING, SAMPLES, CATALOG CUTOUTS, ETC. TO BE APPROVED BY THE ARCHITECT BEFORE FINAL EXECUTION.

4. REFER TO MECHANICAL, PLUMBING DRAWING FOR AN EXACT LOCATION AND SIZES OF ALL MECHANICAL ELEMENTS SHOWN ON CEILING AND ROOF PLANS.

5. LIGHTING FIXTURE TO BE COORDINATED WITH AN ARCHITECT.

6.ANY DISCREPANCY ON SITE AND ON SHOP DRAWINGS, REFER TO CONSULTING ARCHITECT.

7. FOR DOORS, WINDOWS AND ROOM FINISHING SCHEDULE REFER TO DRAWING NO.___

8. CONTRACTOR SHALL VERIFY ALL STRUCTURAL CONDITIONS AND DETAILS PRIOR TO FINAL EXECUTION AND TO ANY DEMOLITION.

9. FOR ALL PERMANENT STRUCTURAL ELEMENTS, REFER TO STRUCTURAL DRAWINGS.

10. MINIMUN PARKING SPACE IS 2.50M WIDTH AND 5.50M LENGTH.

11.

12. INSTALLATION OF ALL MECHANICAL, ELECTRICAL AND PLUMBING ELEMENTS SHALL BE REFER TO MANUFACTURER'S MANUAL.

13. OR UNLESS OTHERWISE BE SPECIFIED

THE INTERIOR DESIGN:
FOR THE FOLLOWING ITEMS:
-CEILING
-DOOR & WINDOW
-FINISHING
-TOILET (WALL TILLING)
-SKYLIGHT
-HANDRAILS

KEYPLAN:

OFFICIAL STAMP:

- [ ] FINAL
- [ ] FOR CONSTRUCTION
- [ ] AS-BUILT
- [ ] APPROVED AS NOTED
- [ ] FOR MUNICIPALITIES
- [ ] OTHERS

DISCIPLINE:
A R C H I T E C T U R E

PROJECT:
فيلا سكنية

OWNER:
سعود محمد سعود المسعود

ALJEEL ARCHITECTS
Design - Project Management - Supervision
6071 King Abdulaziz.Rd- Riyadh - Saudi Arabia
Tel:+966-11-269-0811
WWW.ALJEEL-ARCH.COM

DRAWING TITLE: SECTION A-A

SHEET NO.: A112

SCALE: 1 : 120

DESIGNED BY:	APPROVED BY:	DRAWN BY:	DATE:
Arch. Saleh	Arch. Saleh	Utman	06/02/21
PROJECT NO.:	**STATUS:**	**REVISION**	**CODE:**
Al-Jeel 104	Initial Presentation	---	

7/14/2024 10:58:23 AM

C:\Users\Mohammed\ALJEEL ARCHITECTS Dropbox\design\Aljeel office Dropbox\Running Projects\213-فيلا سعود\Design\Arch\Rvt\VILLA SAUD UPDATE NEW FOR BAADIYA.rvt

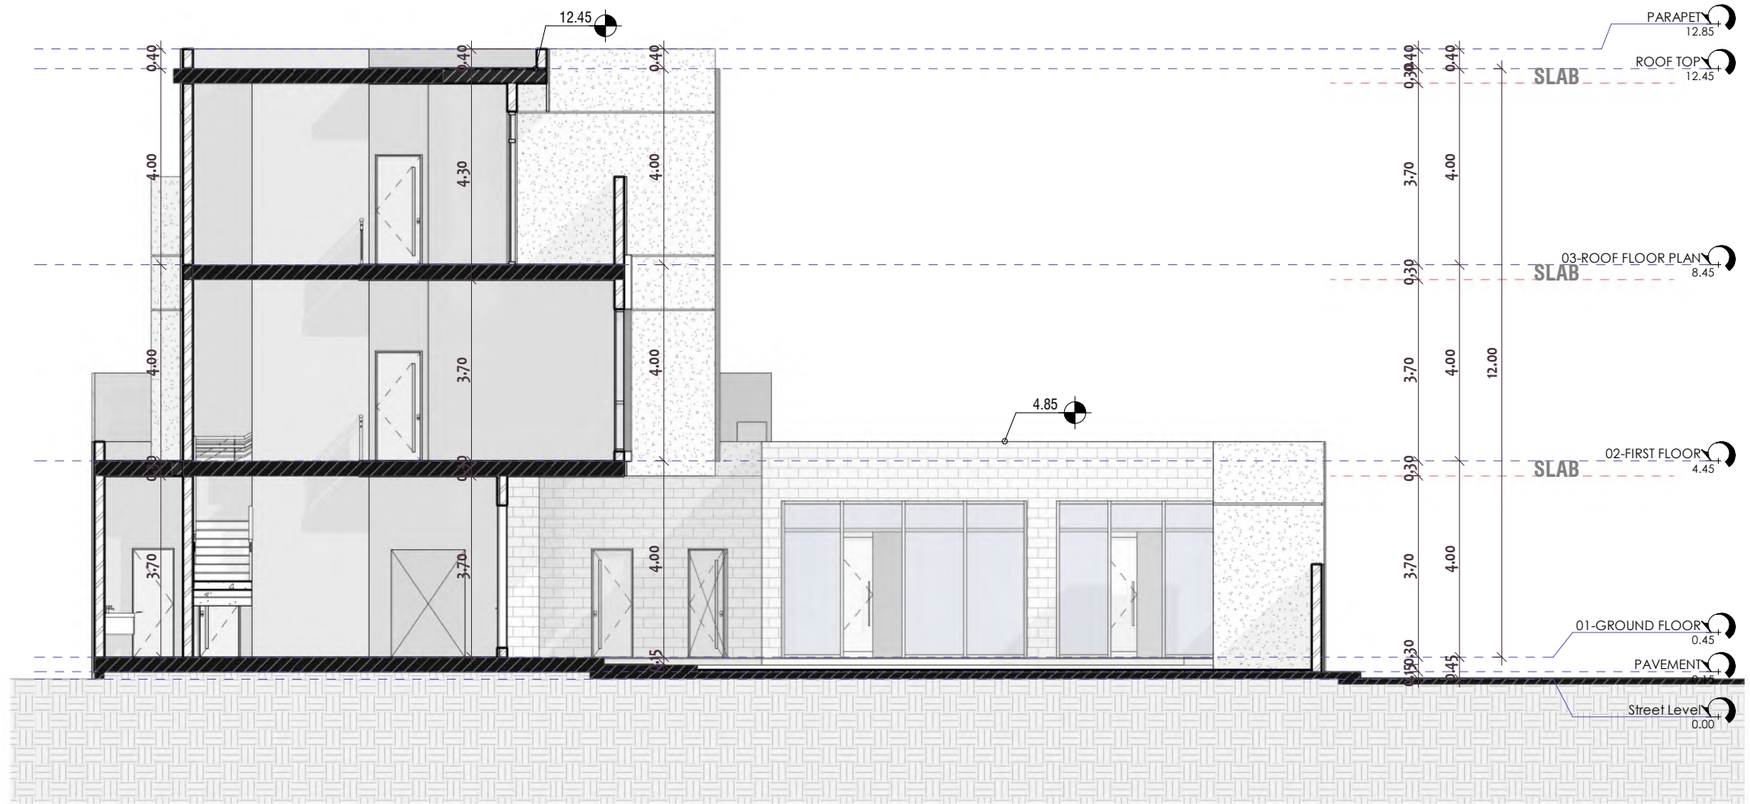

GENERAL NOTES:

1. ALL DIMENSION SHOWN HEREIN ARE ALL IN METERS, UNLESS OR OTHERWISE IT IS SPECIFIED

2. WINDOWS AND WINDOW SCREEN OPENING ON THE JOBSITE AND SUBMIT THE SHOP DRAWINGS PRIOR TO FABRICATION AND INSTALLTION.

3. ALL SHOP DRAWING, SAMPLES, CATALOG CUTOUTS, ETC. TO BE APPROVED BY THE ARCHITECT BEFORE FINAL EXECUTION.

4. REFER TO MECHANICAL, PLUMBING DRAWING FOR AN EXACT LOCATION AND SIZES OF ALL MECHANICAL ELEMENTS SHOWN ON CEILING AND ROOF PLANS.

5. LIGHTING FIXTURE TO BE COORDINATED WITH AN ARCHITECT.

6.ANY DISCREPANCY ON SITE AND ON SHOP DRAWINGS, REFER TO CONSULTING ARCHITECT.

7. FOR DOORS, WINDOWS AND ROOM FINISHING SCHEDULE REFER TO DRAWING NO.___

8. CONTRACTOR SHALL VERIFY ALL STRUCTURAL CONDITIONS AND DETAILS PRIOR TO FINAL EXECUTION AND TO ANY DEMOLITION.

9. FOR ALL PERMANENT STRUCTURAL ELEMENTS, REFER TO STRUCTURAL DRAWINGS.

10. MINIMUN PARKING SPACE IS 2.50M WIDTH AND 5.50M LENGTH.

11.

12. INSTALLATION OF ALL MECHANICAL, ELECTRICAL AND PLUMBING ELEMENTS SHALL BE REFER TO MANUFACTURER'S MANUAL.

13. OR UNLESS OTHERWISE BE SPECIFIED

THE INTERIOR DESIGN:
FOR THE FOLLOWING ITEMS:
-CEILING
-DOOR & WINDOW
-FINISHING
-TOILET (WALL TILLING)
-SKYLIGHT
-HANDRAILS

KEYPLAN:

OFFICIAL STAMP:

- [ ] FINAL
- [ ] FOR CONSTRUCTION
- [ ] AS-BUILT
- [ ] APPROVED AS NOTED
- [ ] FOR MUNICIPALITIES
- [ ] OTHERS

DISCIPLINE:
ARCHITECTURE

PROJECT:
فيلا سكنية

OWNER:
سعود محمد سعود المسعود

ALJEEL ARCHITECTS
Design - Project Management - Supervision
6071 King Abdulaziz.Rd- Riyadh - Saudi Arabia
Tel:+966-11-269-0811
WWW.ALJEEL-ARCH.COM

DRAWING TITLE:
SECTION B-B

SHEET NO.: A113
SCALE: 1 : 110

DESIGNED BY:	APPROVED BY:	DRAWN BY:	DATE:
Arch. Saleh	Arch. Saleh	Utman	06/02/21
PROJECT NO.:	STATUS:	REVISION	CODE:
Al-Jeel 104	Initial Presentation	---	

7/14/2024 10:58:28 AM

C:\Users\Mohammed\ALJEEL ARCHITECTS Dropbox\design\Aljeel office Dropbox\Running Projects\213-فيلا سعود\Design\Arch\Rvt\VILLA SAUD UPDATE NEW FOR BAADIYA.rvt

ALJEEL ARCHITECTS

Design - Project Management - Supervision

WWW.ALJEEL-ARCH.COM
6071 King Abdulaziz.rd- Riyadh - Saudi Arabia
Tel:+966-11-269-0811

7/14/2024 10:57:05 AM